

ПРОЕКТНАЯ ДОКУМЕНТАЦИЯ

Индивидуальный жилой дом

Эскизный проект

"Архитектурные решения"

070023-AP



*г-к Анапа
2023г.*

Ведомость листов комплекта марки АР.

Лист	Наименование	Примечание
1	Общие данные.	
2	3D визуализация	
3	3D визуализация	
4	План первого этажа (мебель).	
5	План первого этажа (кладочный).	
6	План кровли	
7	Разрез 1-1	
8	Фасад 1-4, Фасад 4-1	
9	Фасад А-В, Фасад В-А	

Общие указания.

- Проектная документация по объекту «Индивидуальный жилой дом» разработан в стадии "Эскиз" на основании задания на проектирования, утвержденного заказчиком.
- Проект предназначен для строительства в III Б климатическом районе.
- Степень огнестойкости здания II.
Класс здания по функциональной пожарной опасности Ф1.3.
- За нулевую отметку принят уровень чистого пола 1 этажа.
- Наружные стены выполнены из газобетонных блоков с плотностью D500, прочность В 2,5 на клеевом растворе толщиной 350мм. и с эффективным утеплителем пенополистеролом 100 мм.
- Отделка фасадов.
Наружные стены - декоративные панели.
Цоколь - облицовка керамогранитными плитками.
Кровля - металлическая
Окна и витражи - металлопластиковые.

Основные сведения и условия строительства

- климатический район строительства - III Б,
- нормативный вес снегового покрова - 0,00035МПа
- нормативное давление ветра - 0,001 МПа
- расчетная зимняя температура наружного воздуха -13°C
- нормативная глубина промерзания грунтов -0,8
- сейсмичность площадки- 8 баллов

Основные строительные показатели .

Наименование	Площадь, м ²				Стрительный объем, м ³		
	площадь застройки	общая площадь здания	жилая площадь зд-я		подземная часть	надземная часть	общий
Жилой дом	124,0	82,8	55.8				

Архитектор	Ткачев		<i>Индивидуальный жилой дом</i>	070023-AP		
				Стадия	Лист	Листов
				AC	1	
			<i>Общие данные</i>			




			Индивидуальный жилой дом		070023-AP		
Архитектор	Ткачев				Стадия	Лист	Листов
					AC	2	
3D Визуализация							




			Индивидуальный жилой дом	070023-AP		
Архитектор	Ткачев			Стадия	Лист	Листов
				AC	3	
3D Визуализация						

ПЛАН 1-ГО ЭТАЖА

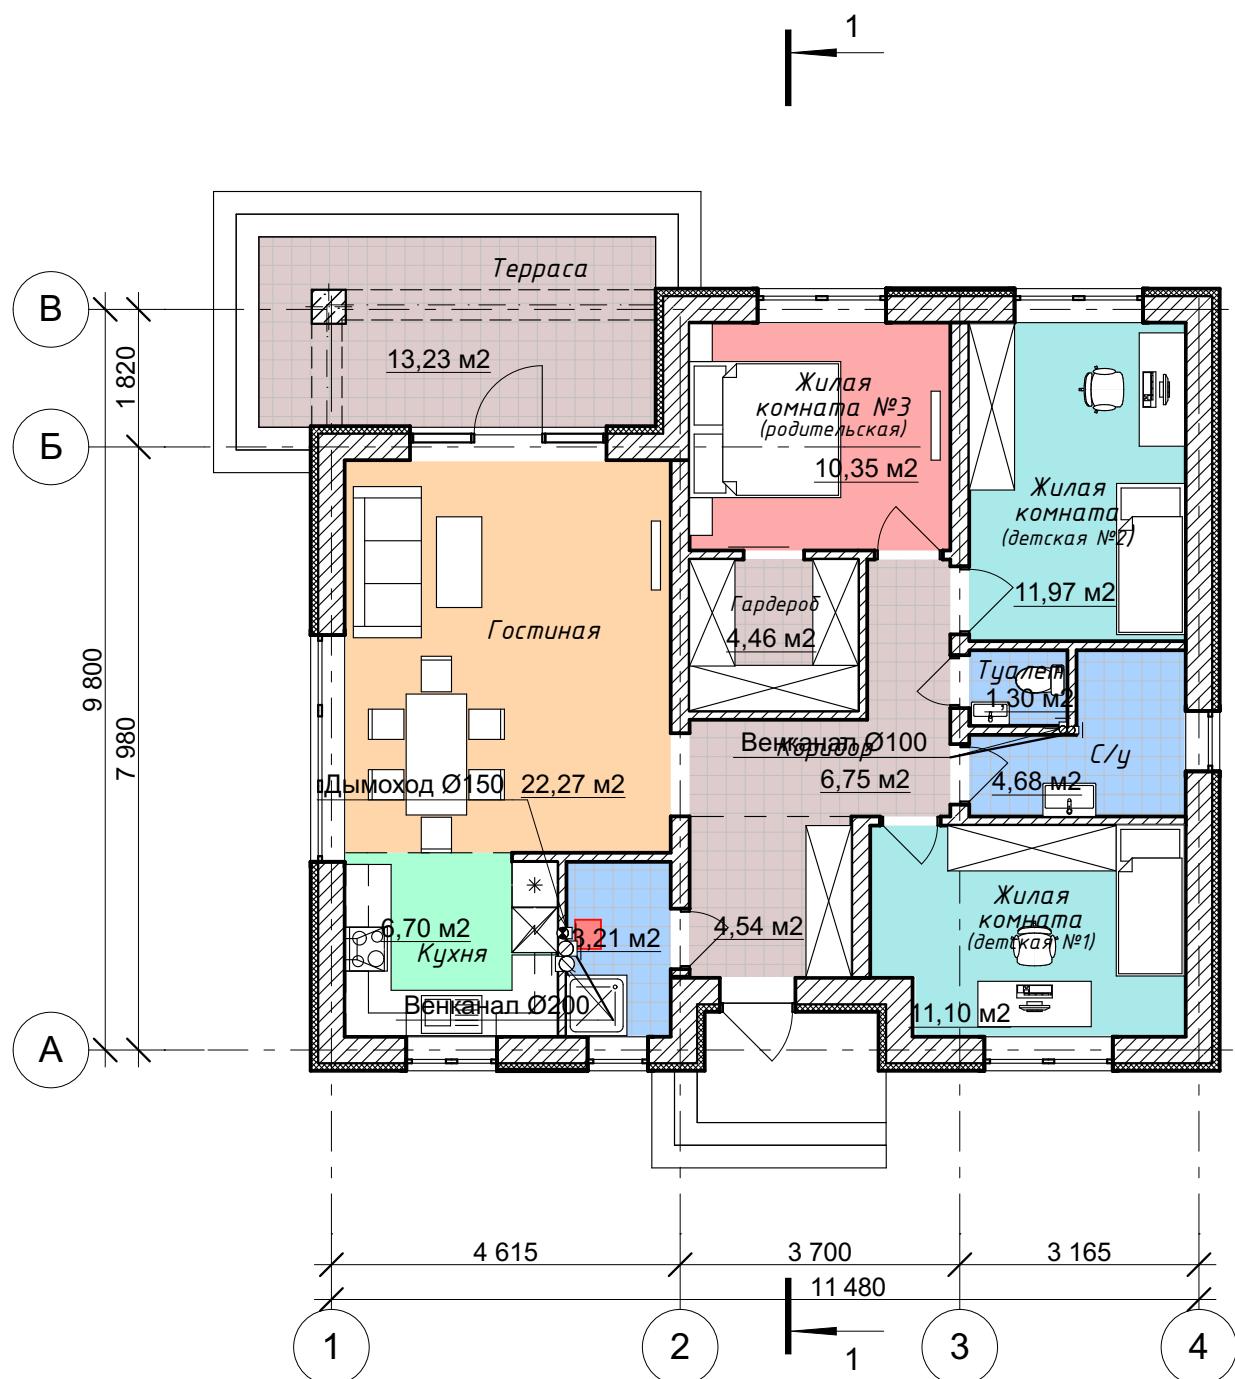


			<i>Индивидуальный жилой дом</i>	070023-AP		
<i>Архитектор</i>	<i>Ткачев</i>			<i>Стадия</i>	<i>Лист</i>	<i>Листов</i>
				AC	4	
			<i>План 1-го этажа (модель)</i>			

ПЛАН 1-ГО ЭТАЖА

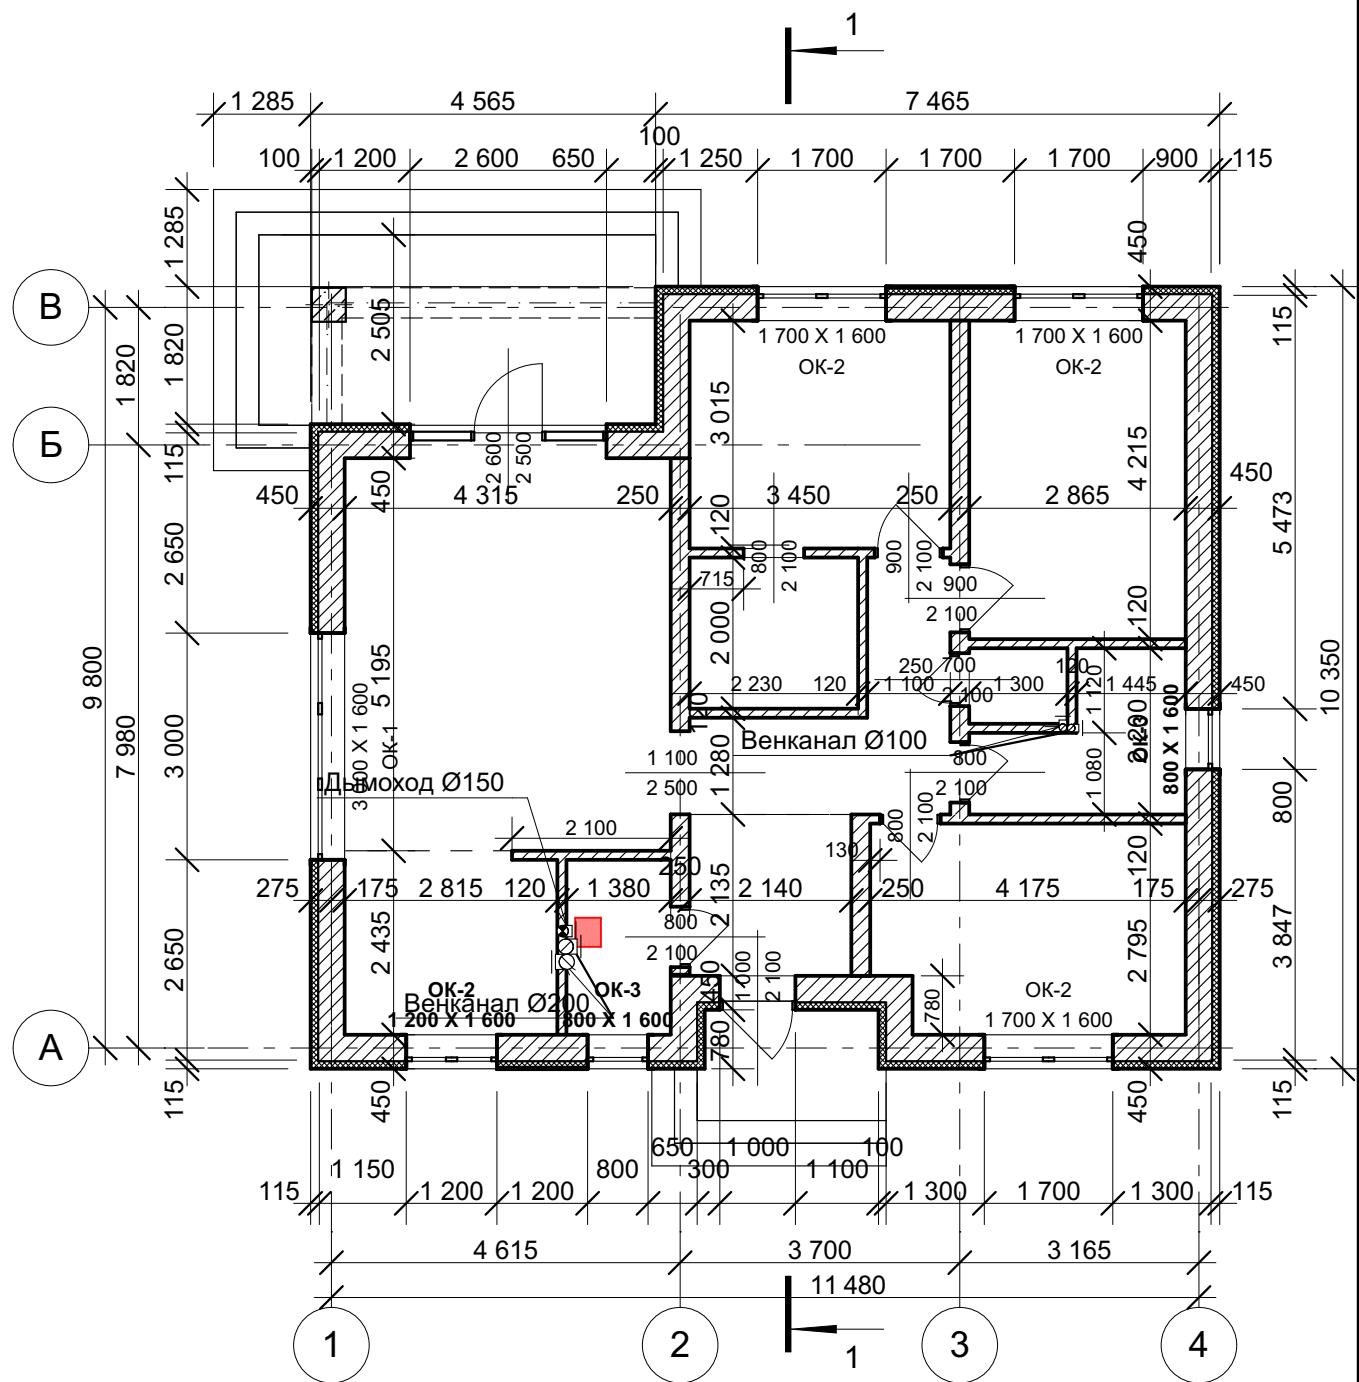


			Индивидуальный жилой дом	070023-AP		
Архитектор	Ткачев			Стадия	Лист	Листов
				AC	5	
			План 1-го этажа (кладочный)			

ПЛАН КРОВЛИ

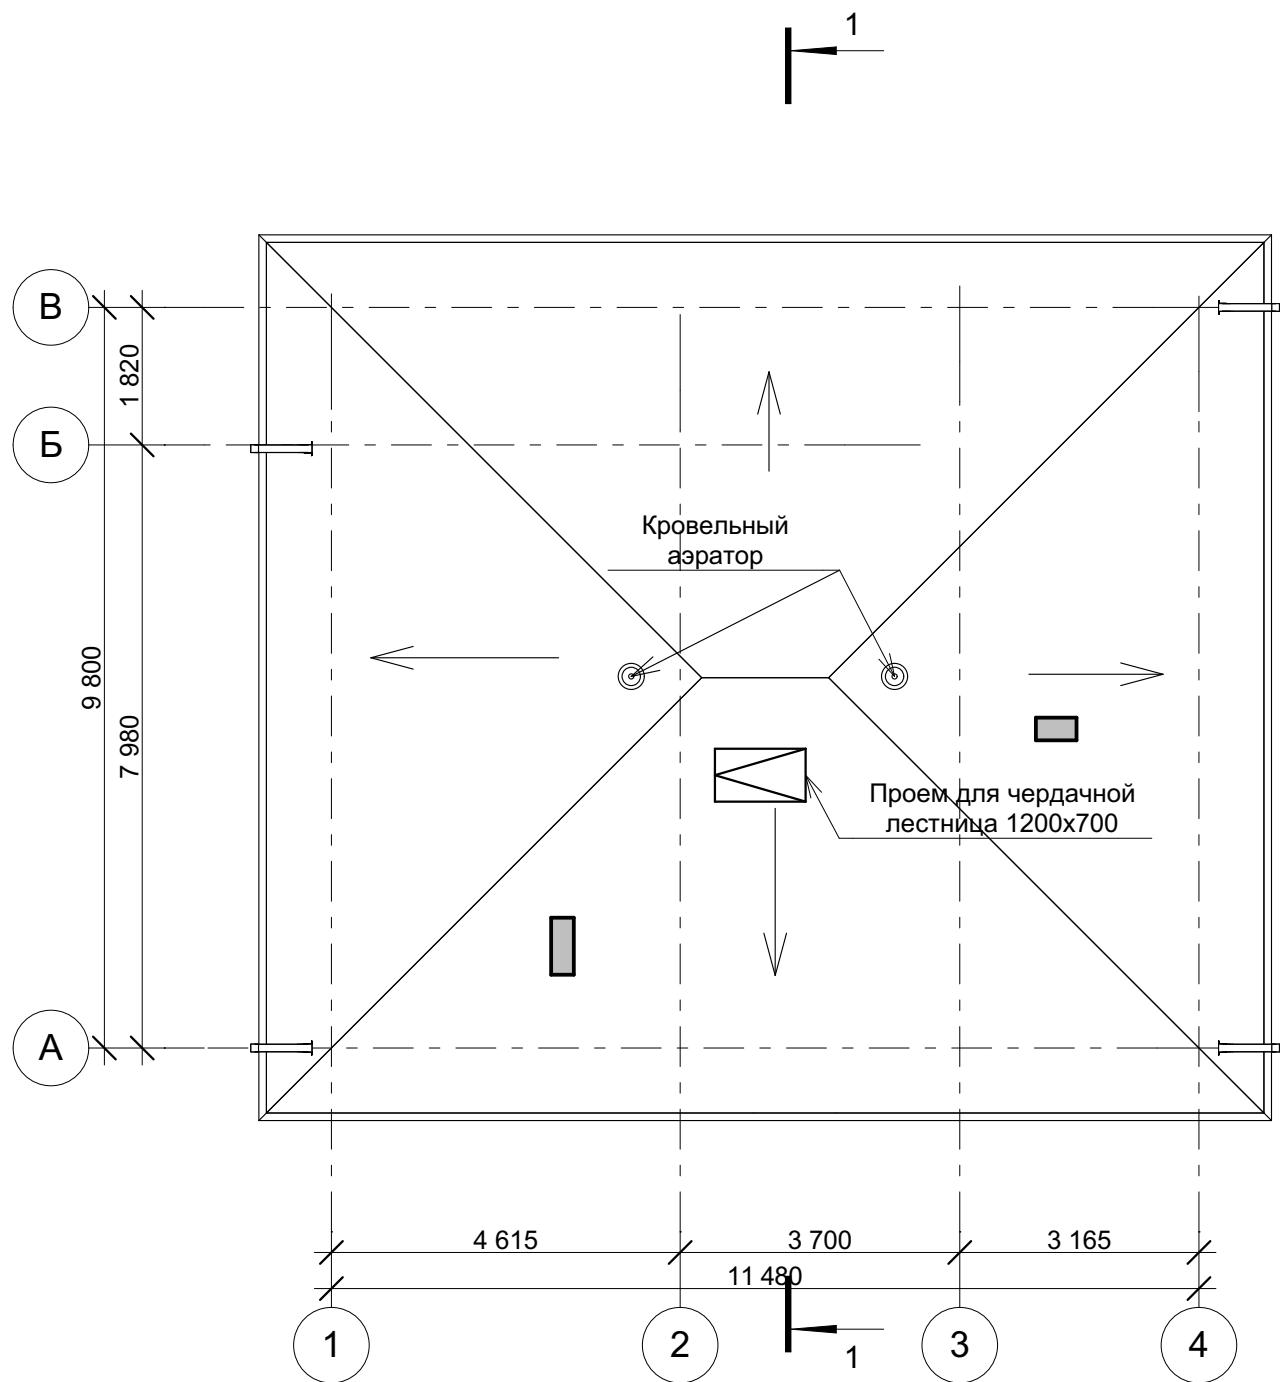

			Индивидуальный жилой дом	070023-AP		
Архитектор	Ткачев					
Стадия			Лист	Листов		
АС			6			
План кровли						

РАЗРЕЗ 1-1

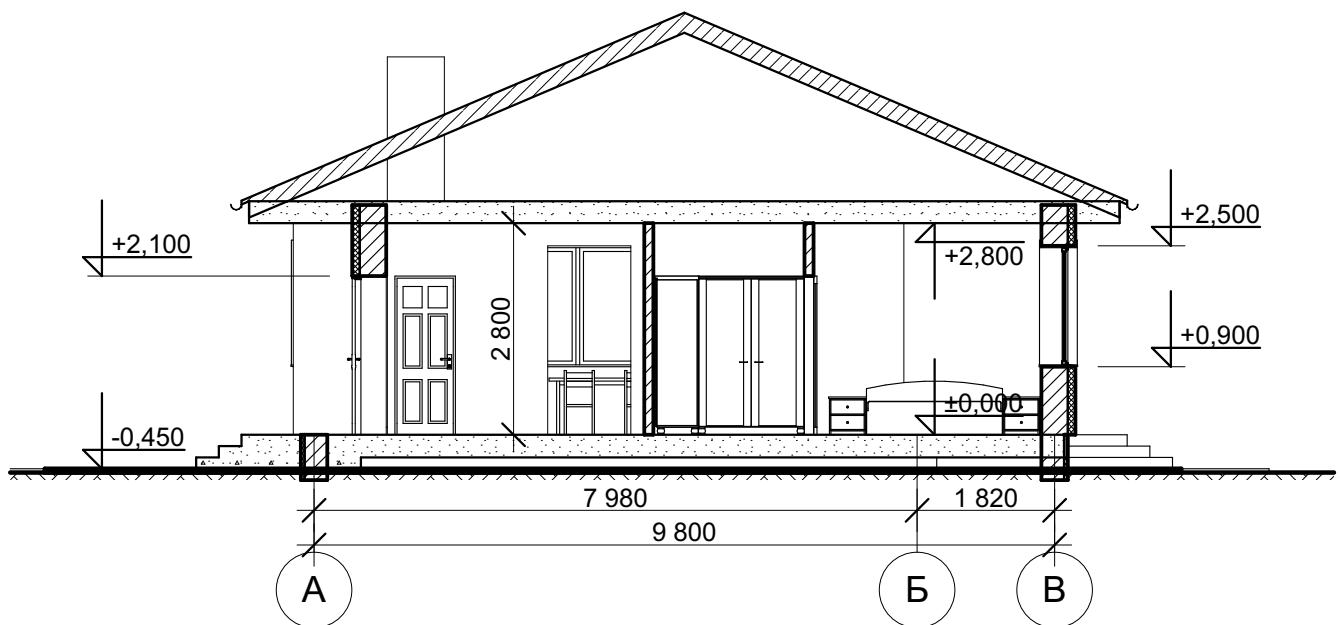


			Индивидуальный жилой дом		070023-AP		
Архитектор	Ткачев					Стадия	Лист
						AC	7
Разрез 1-1							

ФАСАД 1-4




ФАСАД 4-1

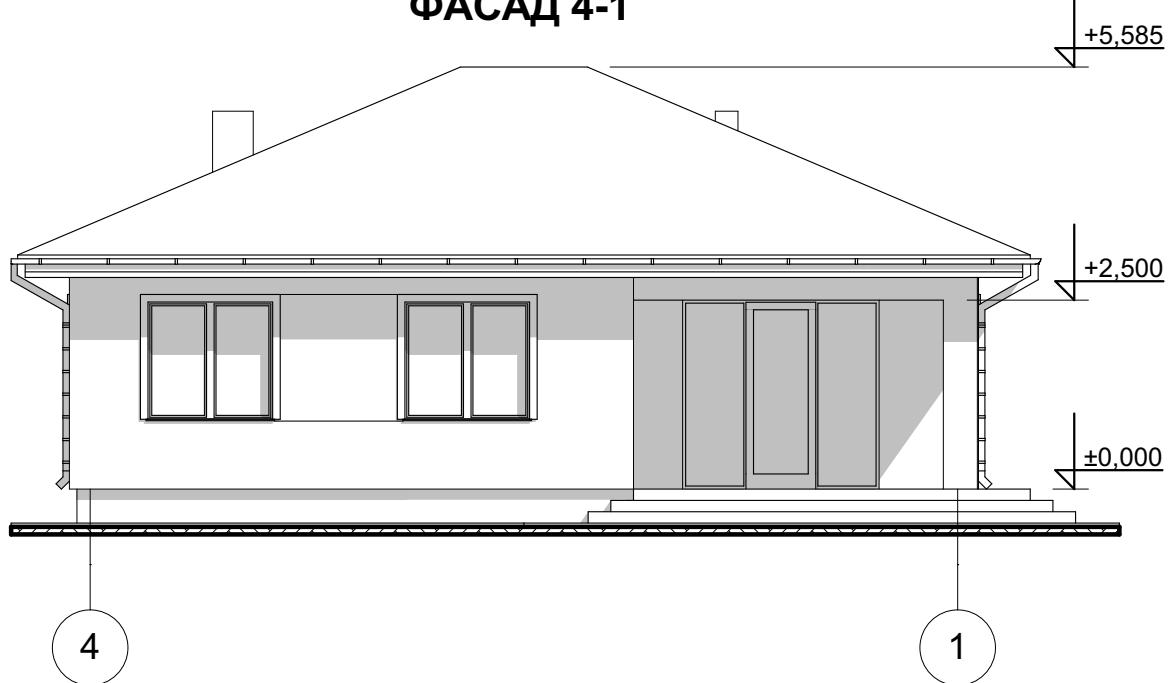


			Индивидуальный жилой дом	070023-AP		
Архитектор	Ткачев			Стадия	Лист	Листов
				АС	8	
Фасад 1-4, 4-1						

ФАСАД А-В

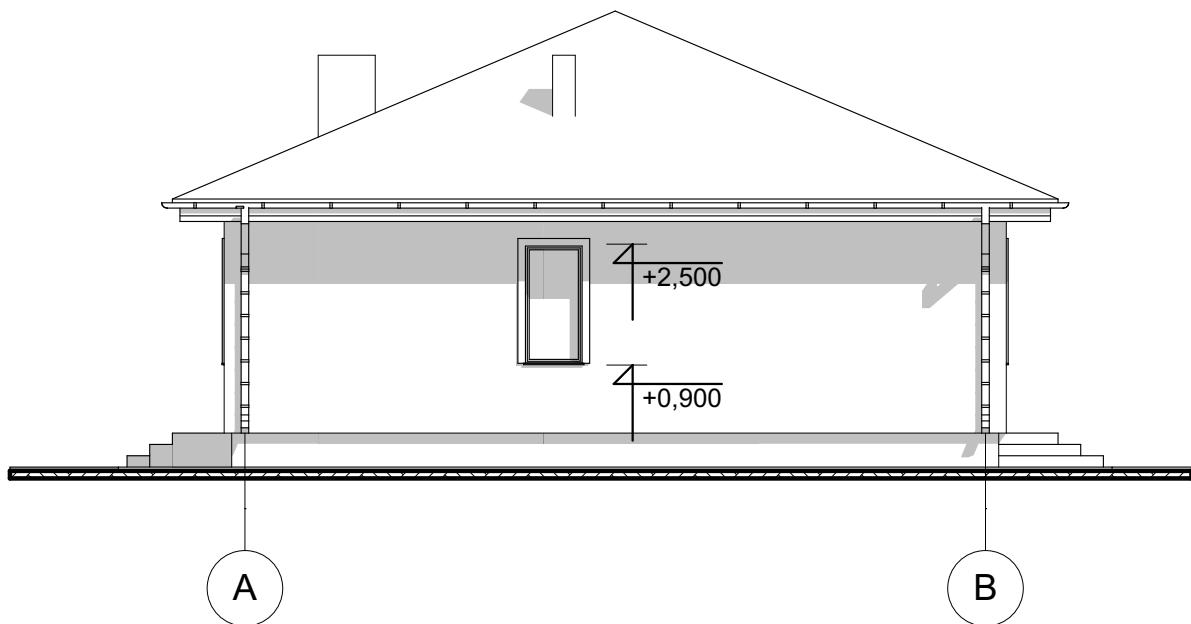

ФАСАД В-А

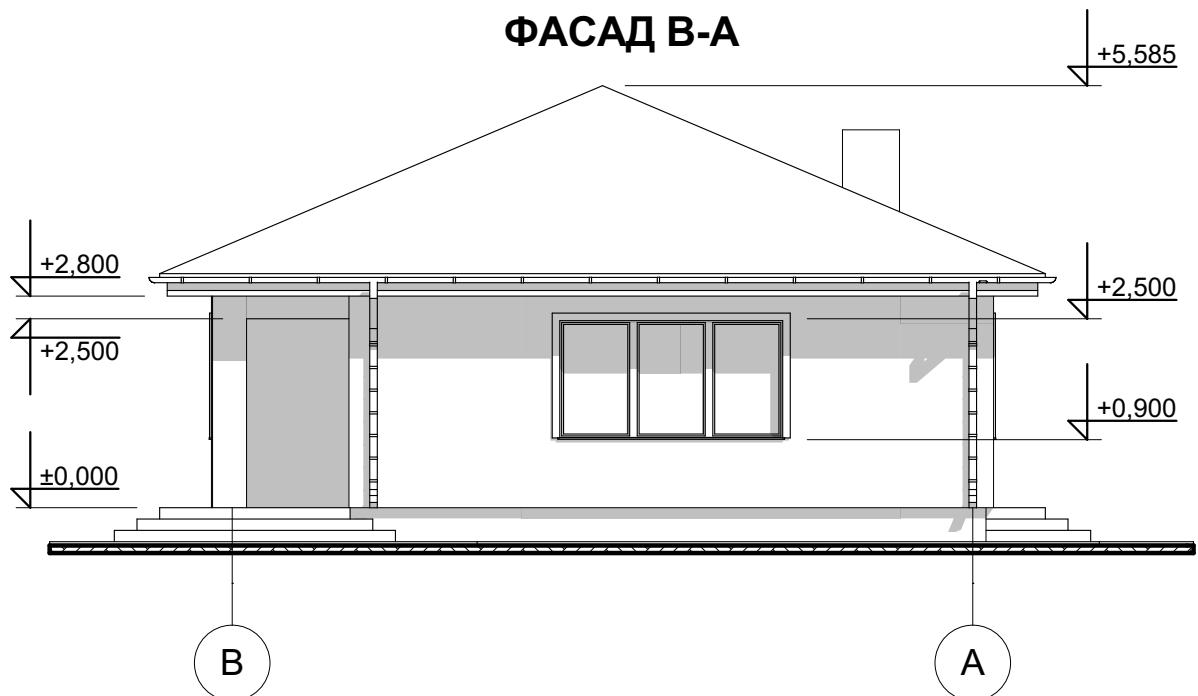

			Индивидуальный жилой дом	070023-AP		
Архитектор	Ткачев			Стадия	Лист	Листов
				AC	9	
Фасад А-Б, Б--А						