

ПРОЕКТНАЯ ДОКУМЕНТАЦИЯ

Индивидуальный жилой дом

Эскизный проект

"Архитектурные решения"

030023-AP



*г-к Анапа
2023г.*

Ведомость листов комплекта марки АР.

Лист	Наименование	Примечание
1	Общие данные.	
2	3D Визуализация	
3	3D Визуализация	
4	План первого этажа. Мебель	
5	План второго этажа. Мебель	
6	План первого этажа. Кладочный	
7	План второго этажа. Кладочный	
8	План кровли	
9	Фасад 1-2, 2-1	
10	Фасад А-В, В-А	
11	Разрез 1-1, 2-2	

Общие указания.

- Проектная документация по объекту «Индивидуальный жилой дом» разработан в стадии "Эскиз" на основании задания на проектирования, утвержденного заказчиком.
- Проект предназначен для строительства в III Б климатическом районе.
- Степень огнестойкости здания II.

Класс здания по функциональной пожарной опасности Ф1.3.

- За нулевую отметку принят уровень чистого пола 1 этажа.

- Наружные стены многослойные выполнены из блоков толщиной 200мм., с эффективным утеплителем 50 мм. и облицовочным кирпичем 120 мм

- Отделка фасадов.

Наружные стены - облицовочный кирпич.

Цоколь - облицовка керамогранитными плитками.

Кровля - металлопрофиль

Окна и витражи - металлопластиковые.

Основные строительные показатели .

Наименование	Площадь, м2				Стрительный объем, м3		
	площадь застройки	общая площадь здания			подземная часть	надземная часть	общий
Жилой дом	127,5	163,6			0	750	750
			<i>Индивидуальный жилой дом</i>				<i>030023-AP</i>
Архитектор	Tкачев		<i>Жилой дом</i>				<i>Стадия</i> <i>Лист</i> <i>Листов</i>
							<i>AC</i> <i>1</i> <i></i>
			<i>Общие данные</i>				




			Индивидуальный жилой дом		030023-AP		
Архитектор	Ткачев		Жилой дом			Стадия	Лист
						AC	2
			3D Визуализация				




			Индивидуальный жилой дом		030023-AP		
Архитектор	Ткачев		Жилой дом		Стадия	Лист	Листов
						AC	3
			3D Визуализация				

ПЛАН 1-ГО ЭТАЖА

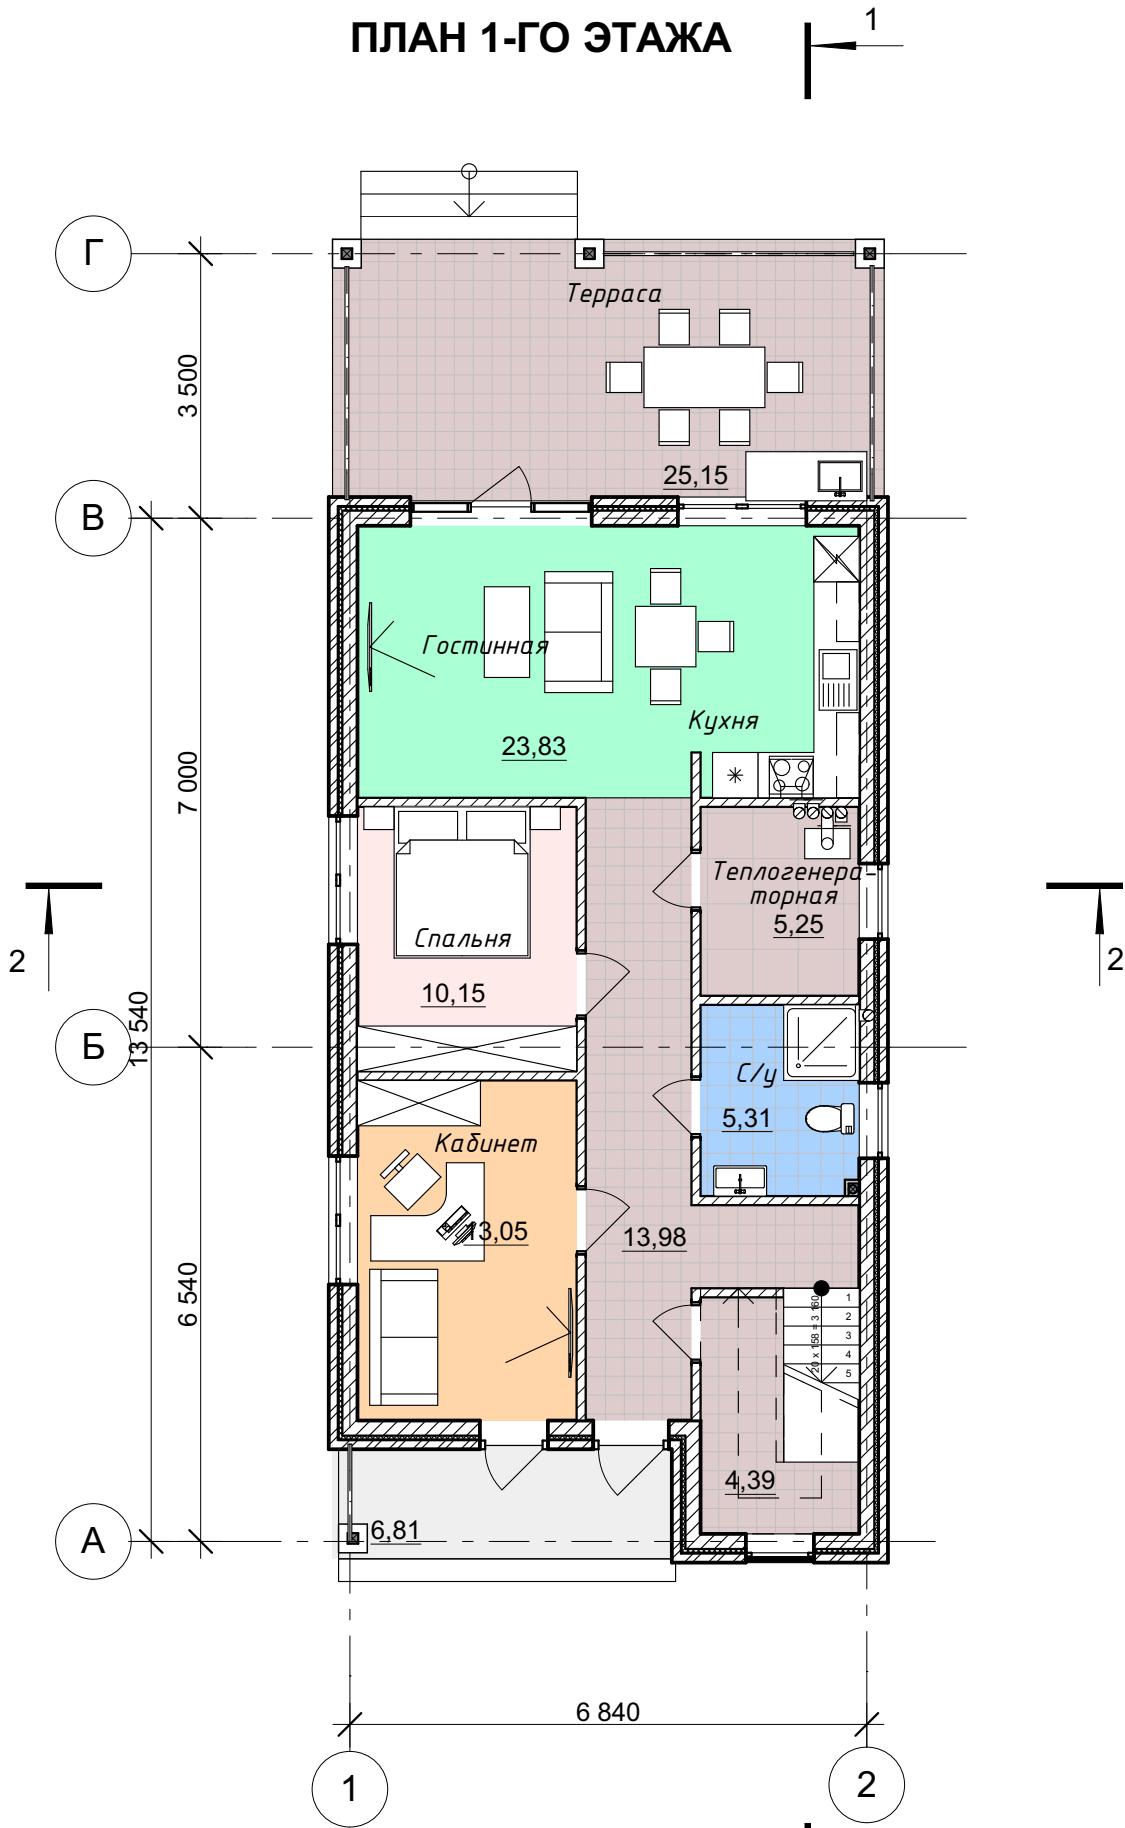


Архитектор	Ткачев	Индивидуальный жилой дом		Стадия	Лист	Листов
Жилой дом				AС	4	
План 1-го этажа						

ПЛАН 2-ГО ЭТАЖА

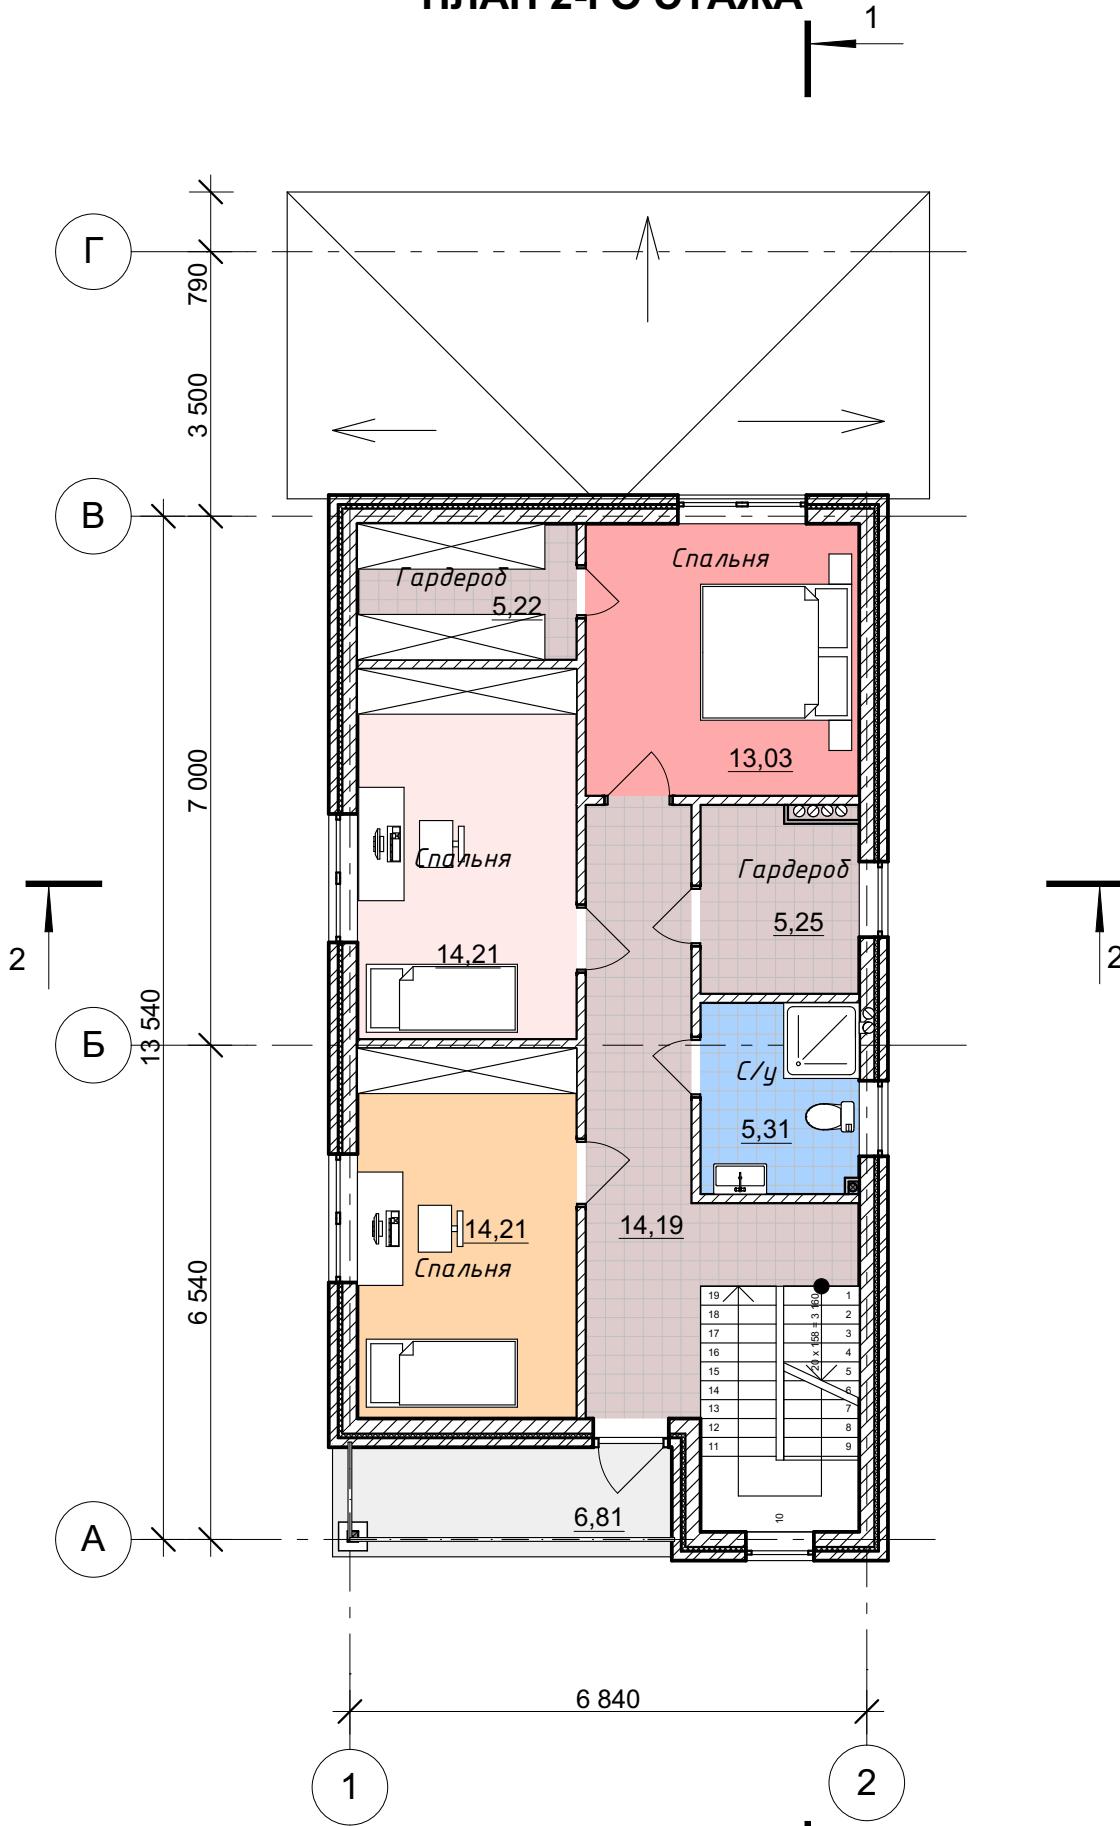


Архитектор	Ткачев	Индивидуальный жилой дом		Стадия	Лист	Листов
Жилой дом		030023-AP		AС	5	
План 2-го этажа						

ПЛАН 1-ГО ЭТАЖА

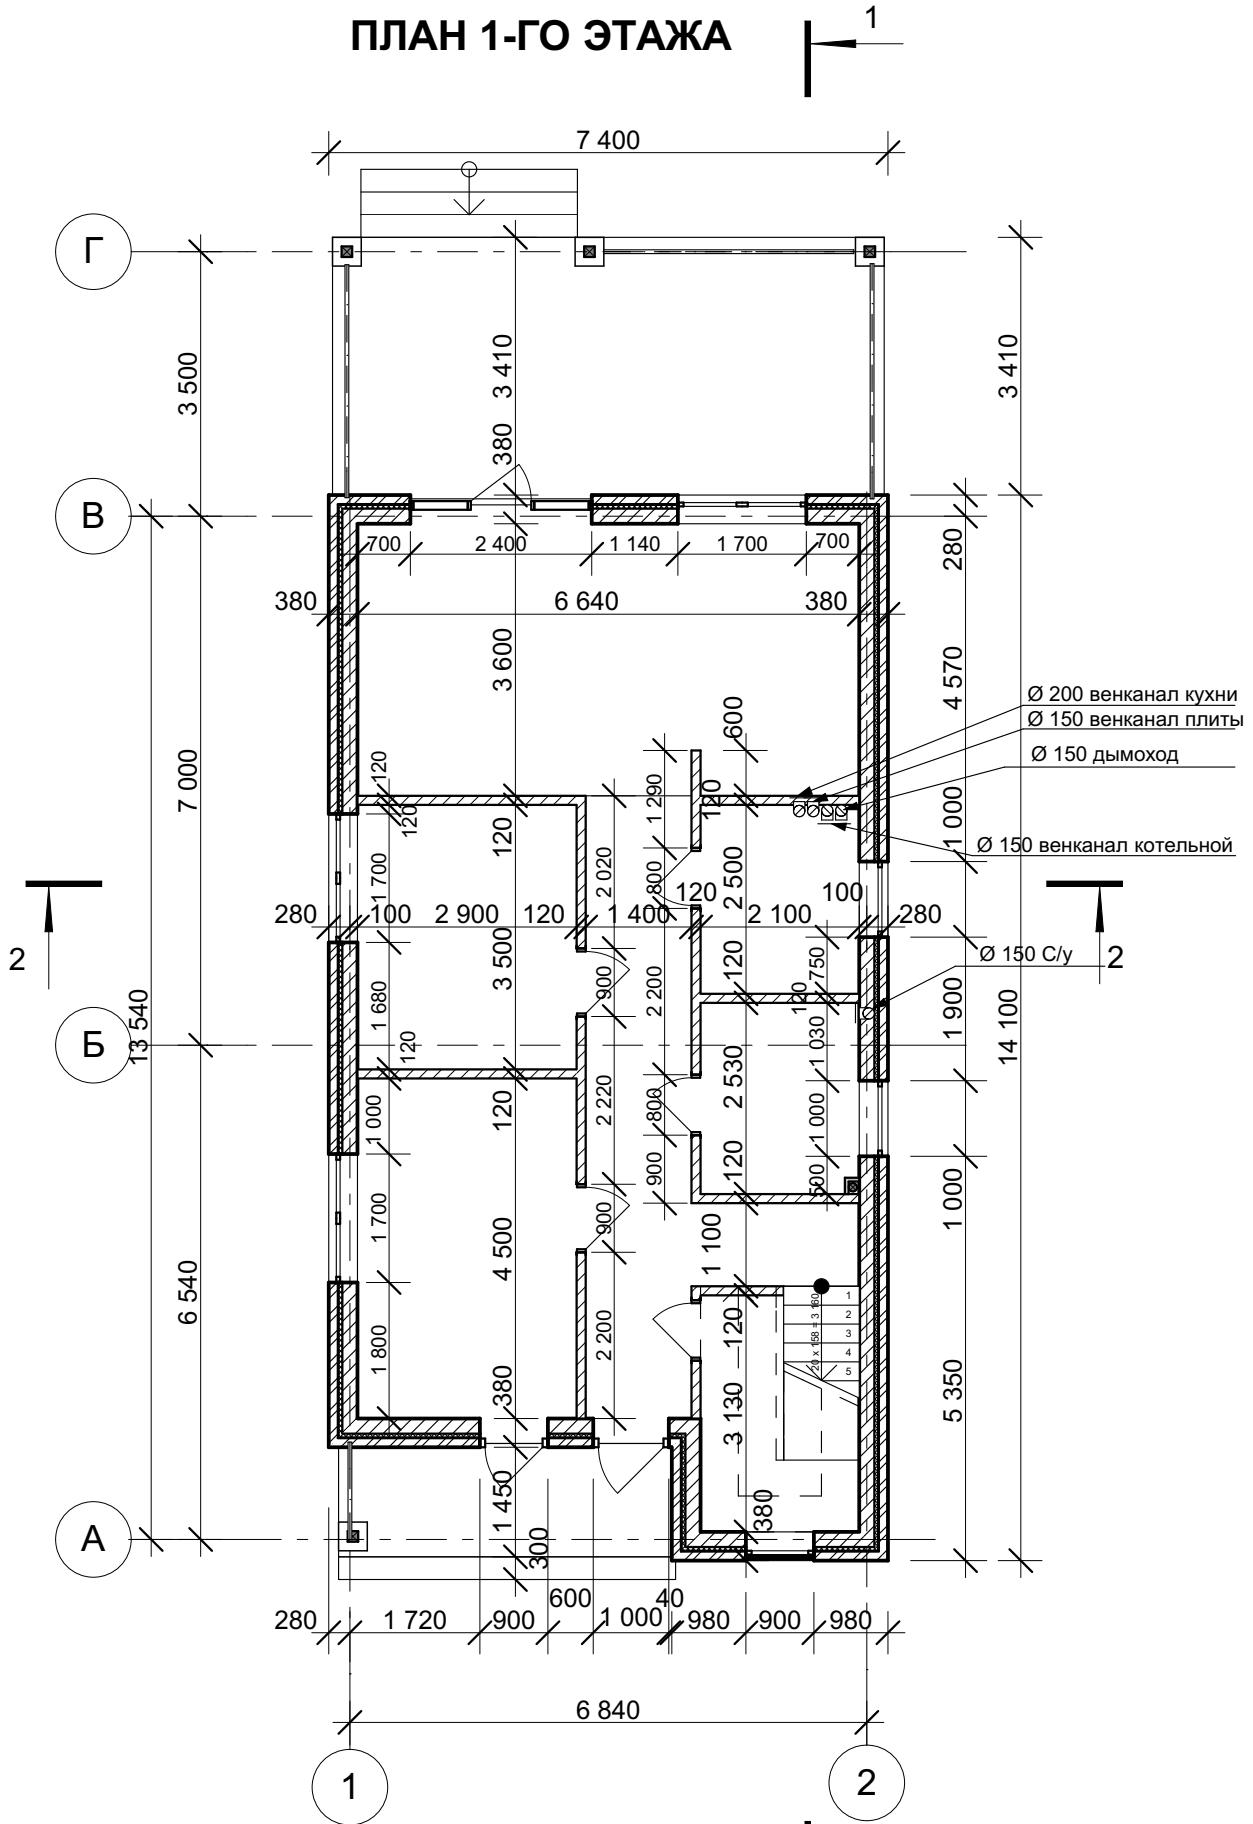


			Индивидуальный жилой дом	1	030023-AP		
Архитектор	Ткачев		Стадия			Лист	Листов
			Жилой дом	AC	6		
			План 1-го этажа - Кладочный				

ПЛАН 2-ГО ЭТАЖА

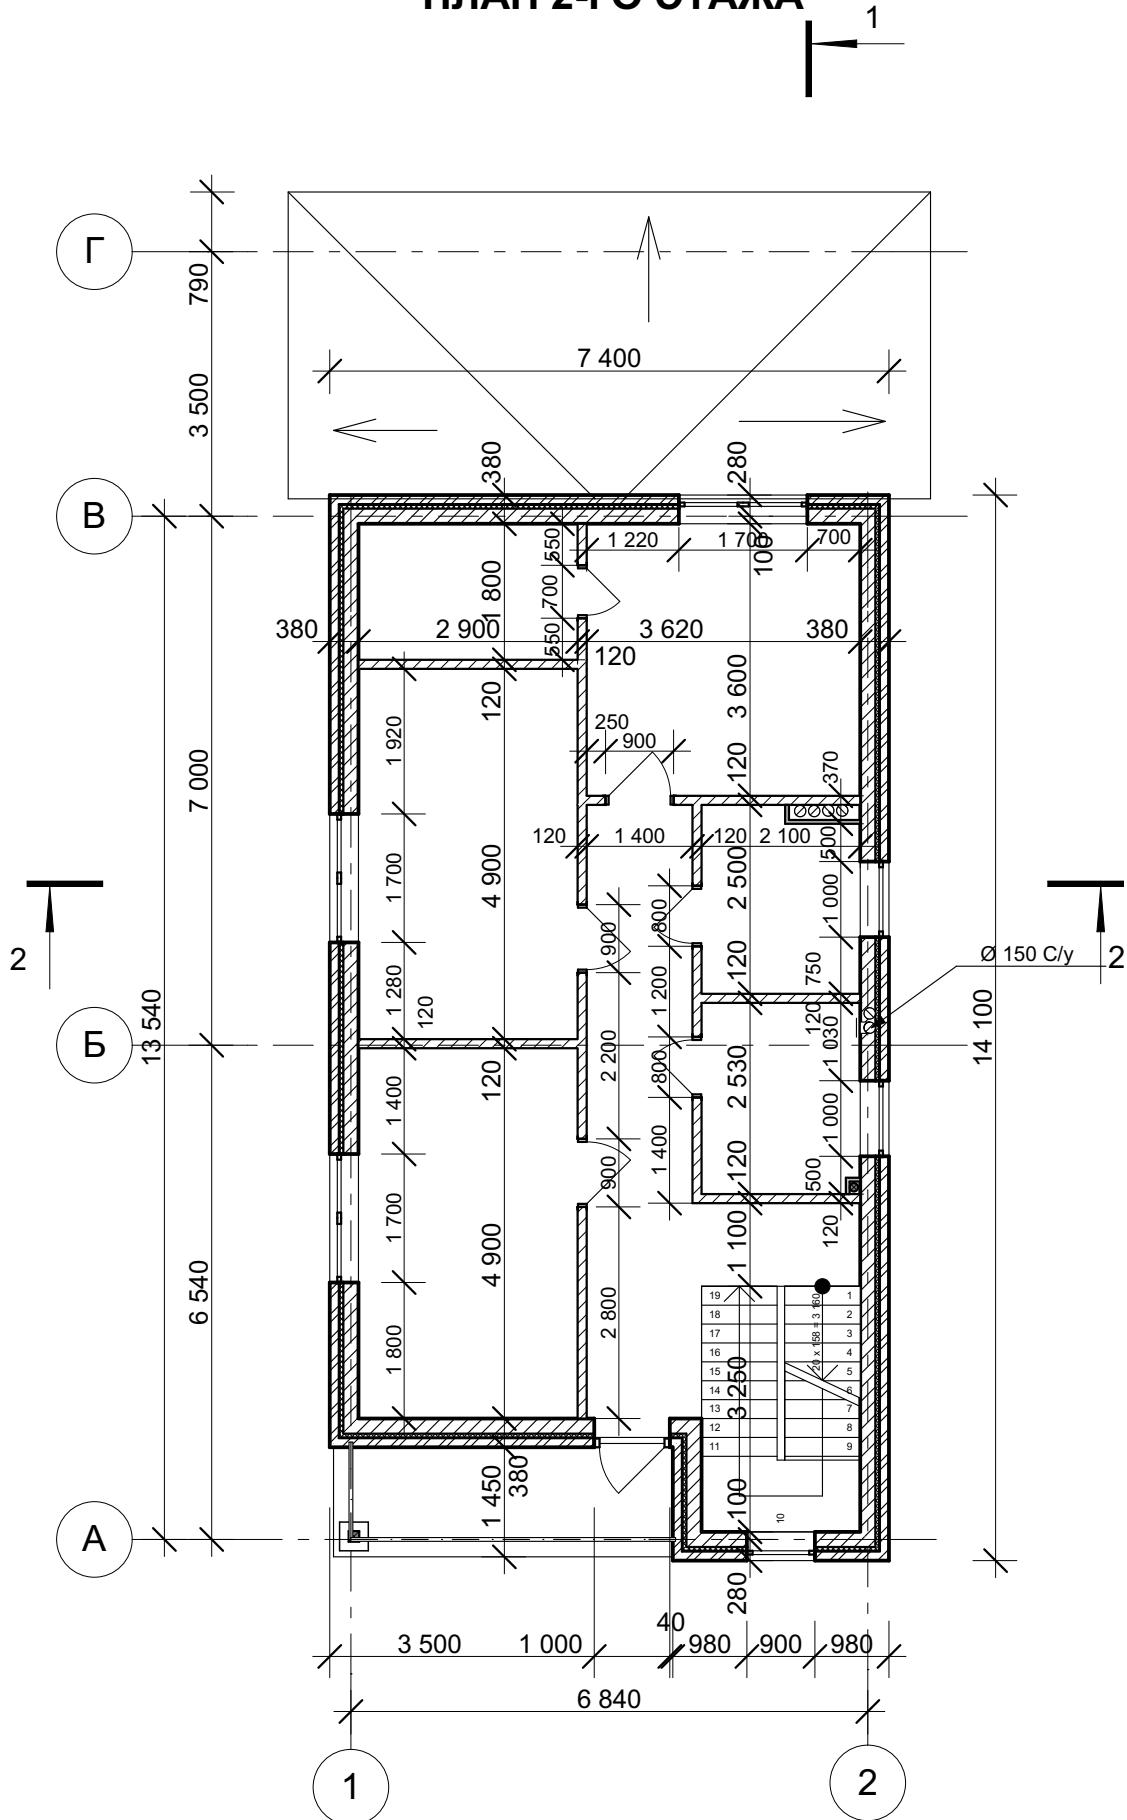


Архитектор	Ткачев	Индивидуальный жилой дом		Стадия	Лист	Листов
		Жилой дом		AС	7	
		План 2-го этажа - Кладочный				

План кровли

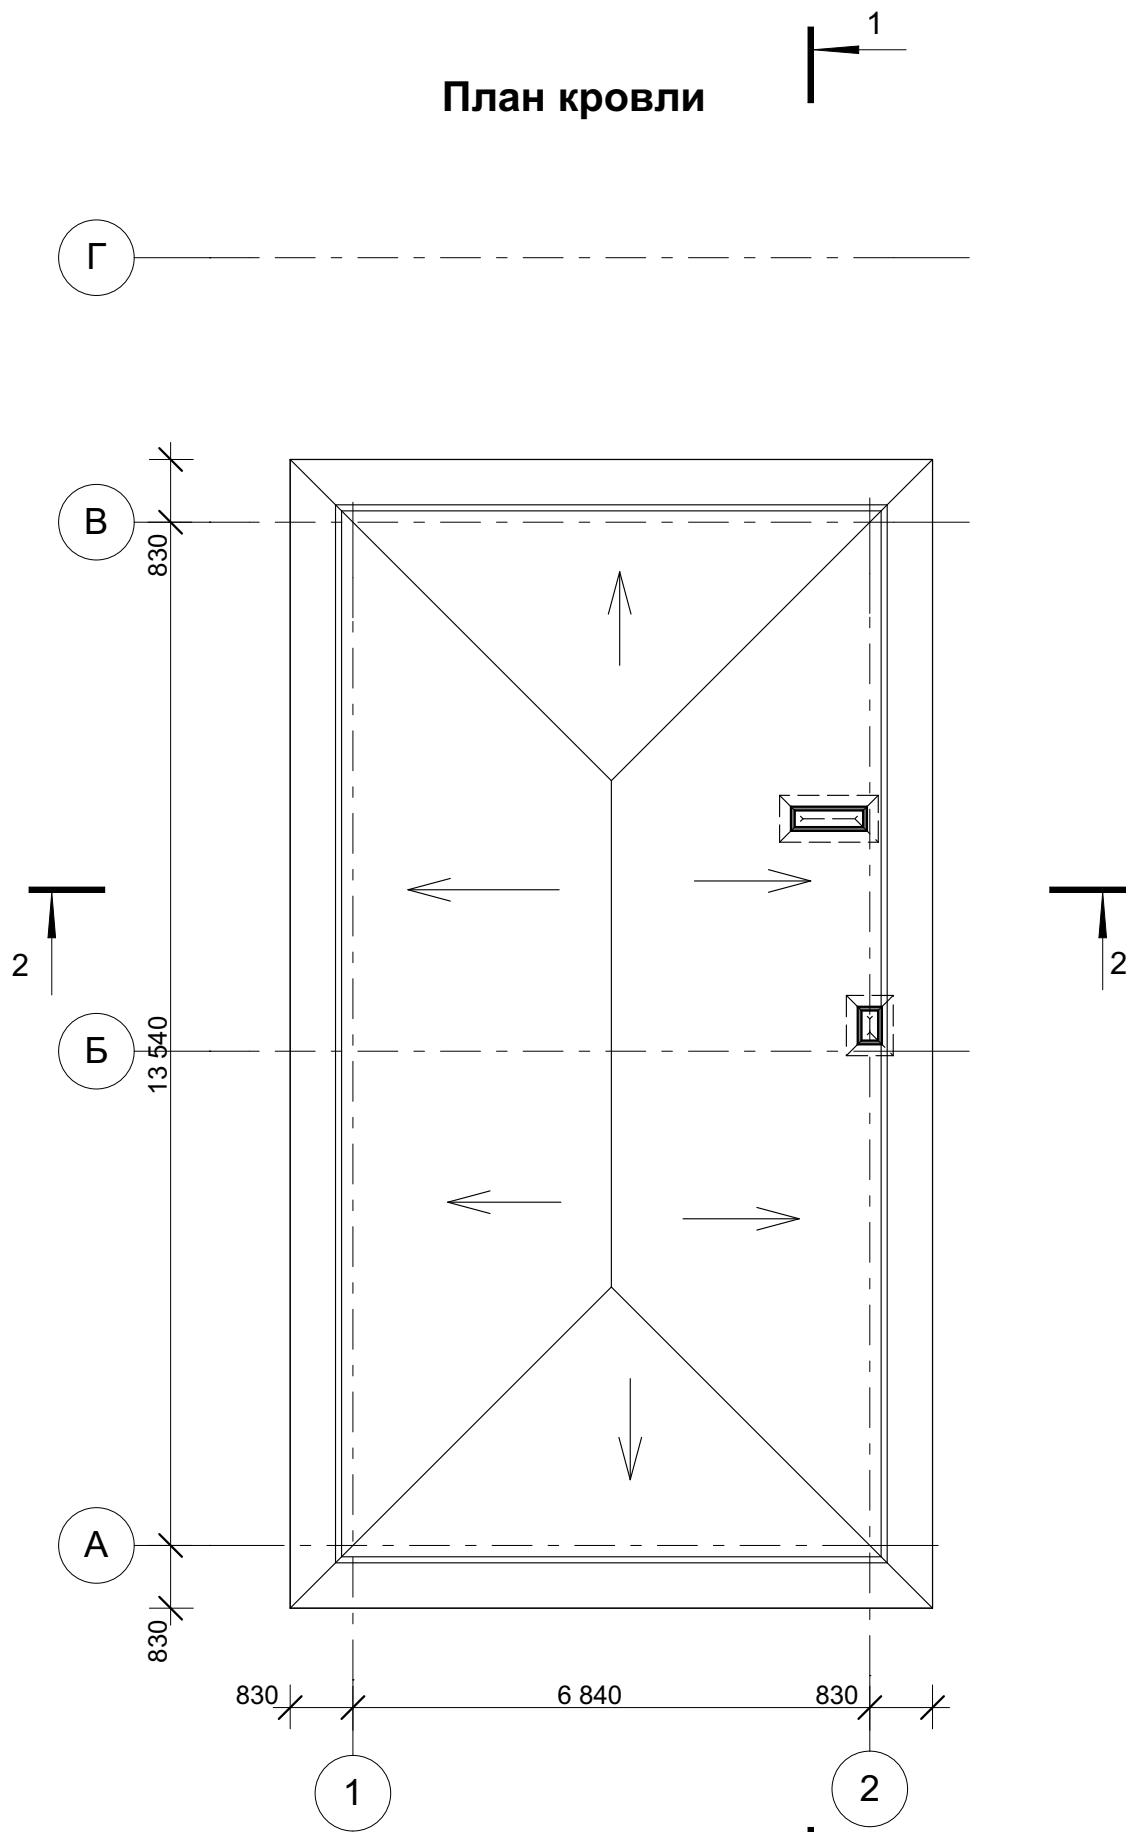


Архитектор	Ткачев	Индивидуальный жилой дом		Стадия	Лист	Листов
		Жилой дом		AС	8	
		План кровли				

ФАСАД 1-2

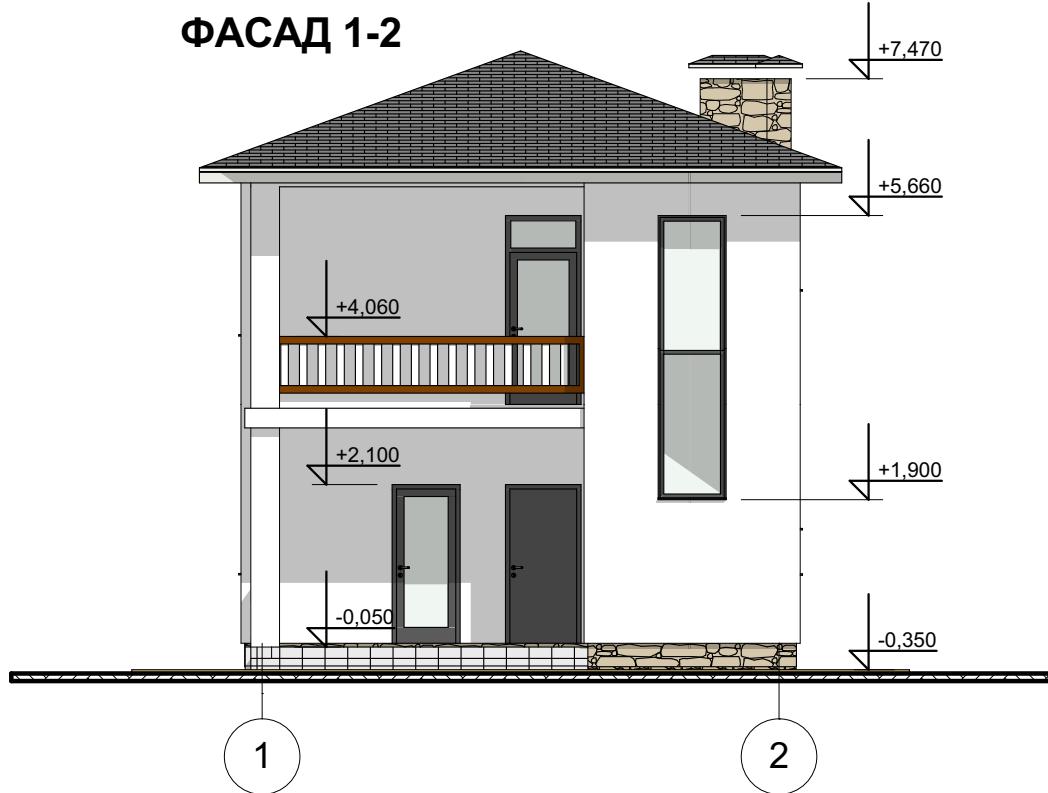


ФАСАД 2-1

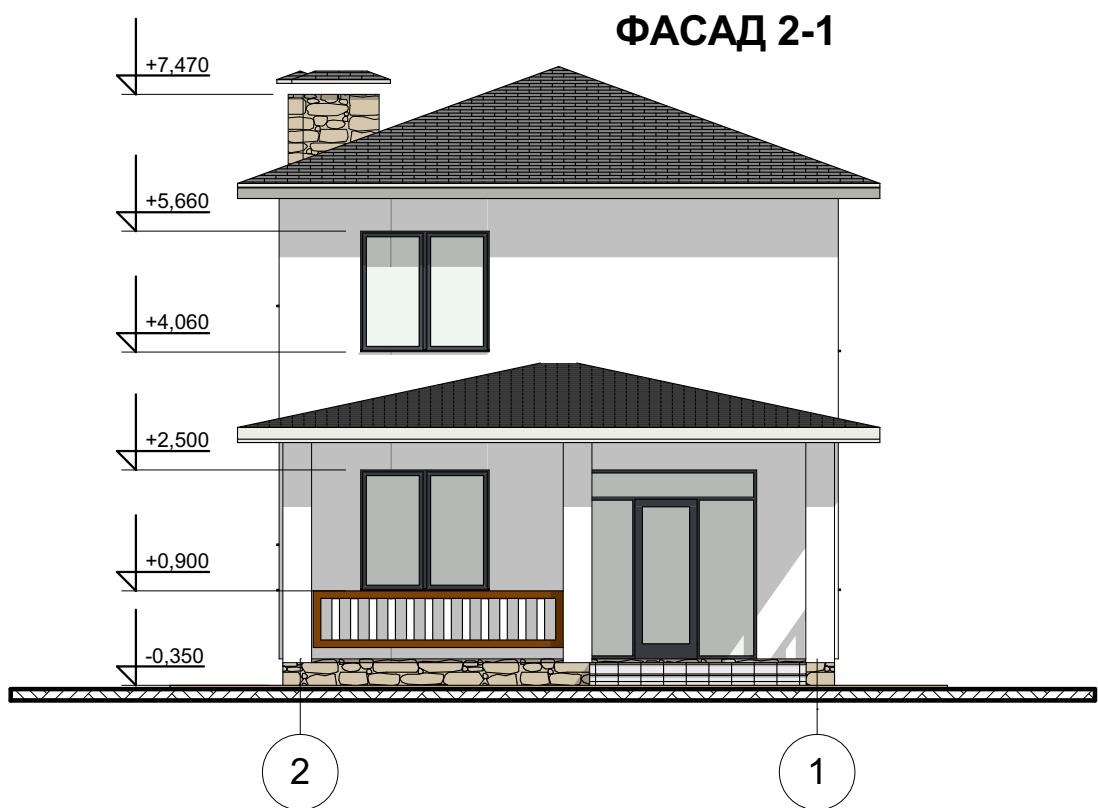

			<i>Индивидуальный жилой дом</i>	030023-AP		
Архитектор	Ткачев		<i>Жилой дом</i>			Стадия
<i>Фасад 1-2, 2-1</i>			Лист			Листов
			AC			


ФАСАД А-В

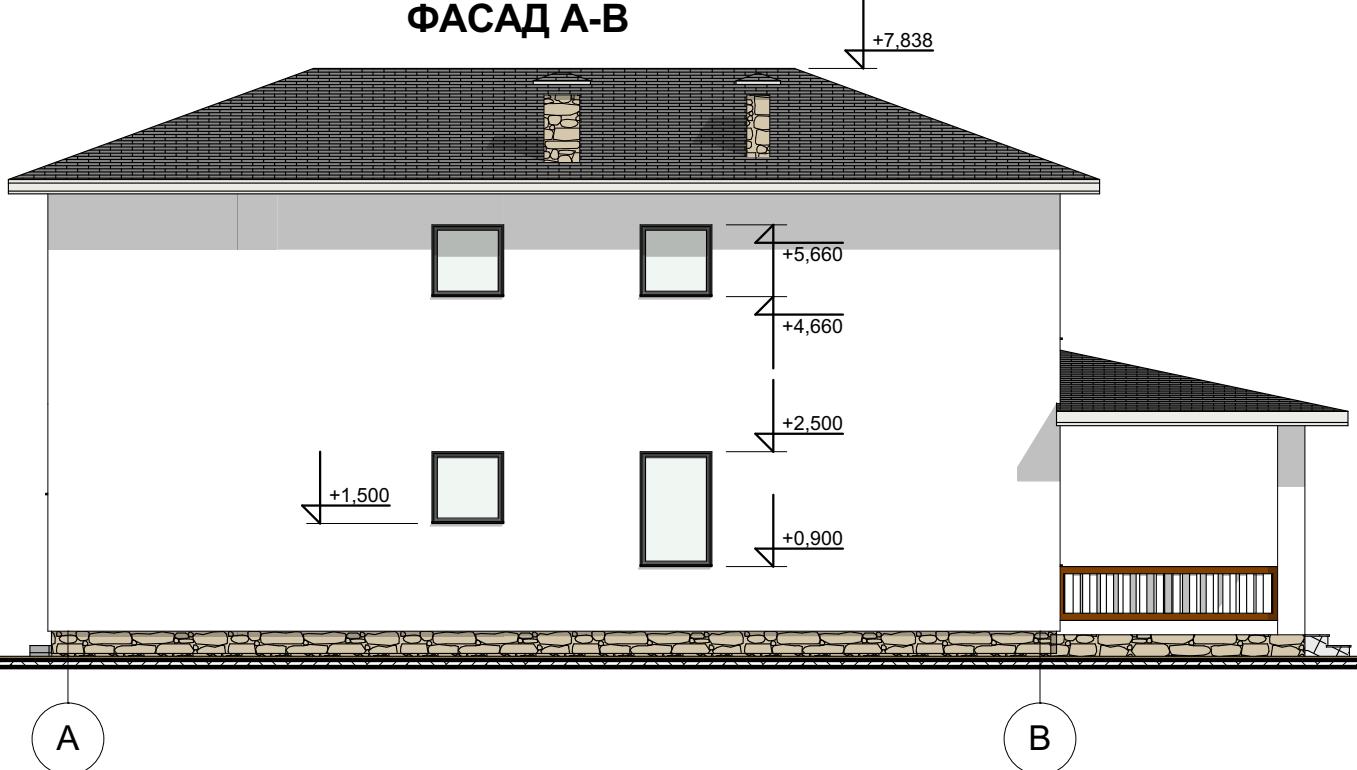

A

B

ФАСАД В-А

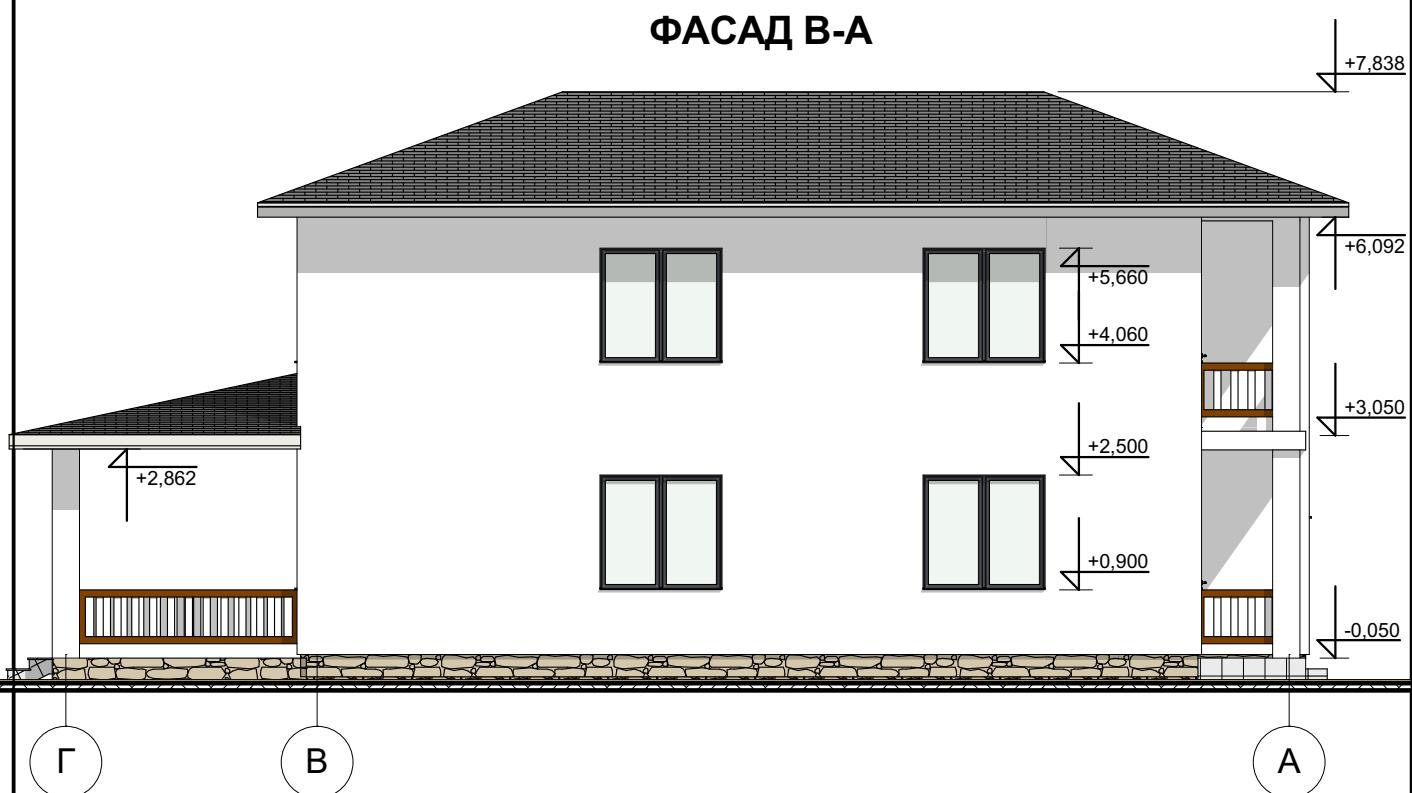


Г

В


А

			Индивидуальный жилой дом	030023-AP		
Архитектор	Ткачев					
Жилой дом			Стадия			Лист
			АС			Листов
Фасад А-В, В-А						

РАЗРЕЗ 1-1

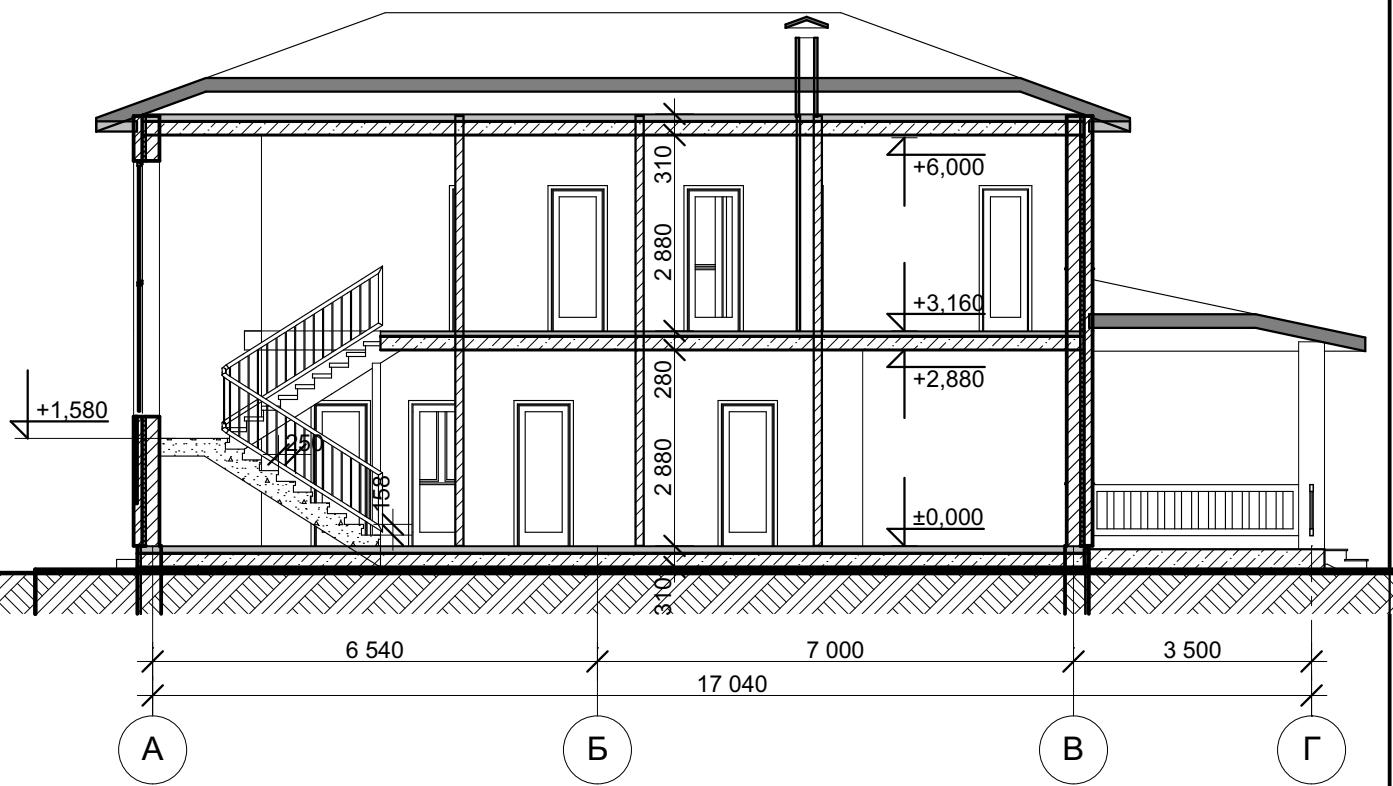

РАЗРЕЗ 2-2

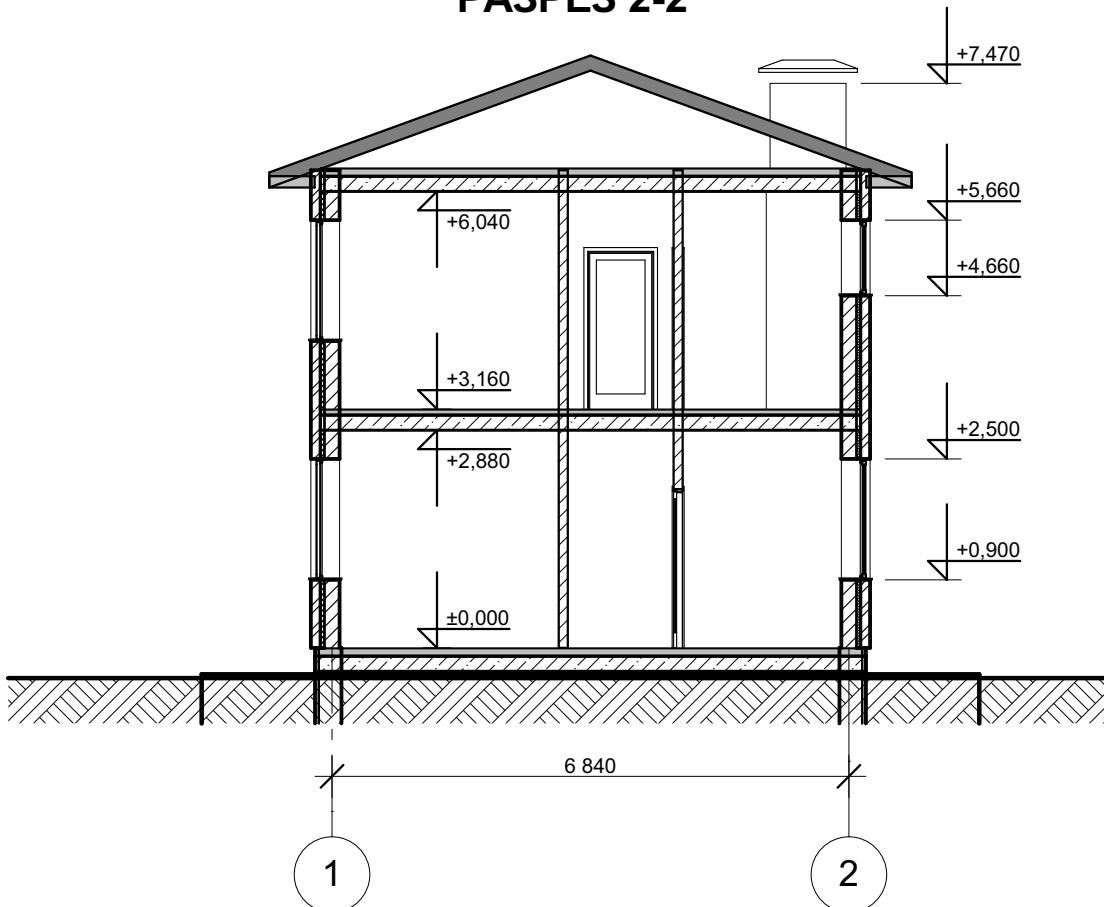

Архитектор	Ткачев	Индивидуальный жилой дом		030023-AP		
		Жилой дом			Стадия	Лист
					AC	11
Разрез 1-1, 2-2						