

# **ПРОЕКТНАЯ ДОКУМЕНТАЦИЯ**

## **Индивидуальный жилой дом**

Эскизный проект  
"Архитектурные решения"  
050023-AP



*г-к Анапа  
2023г.*

# Ведомость листов комплекта марки АР.

Лист	Наименование	Примечание
1	Общие данные.	
2	3D Визуализация	
3	3D Визуализация	
4	План первого этажа. Мебель	
5	План первого этажа. Кладочный	
6	План кровли	
7	Фасад 1-2, 2-1	
8	Фасад А-Г, Г-А	
9	Разрез 1-1	

## Общие указания.

1. Проектная документация по объекту «Индивидуальный жилой дом» разработан в стадии "Эскиз" на основании задания на проектирования, утвержденного заказчиком.

2. Проект предназначен для строительства в III Б климатическом районе.

3. Степень огнестойкости здания II.

Класс здания по функциональной пожарной опасности Ф1.3.

4. За нулевую отметку принят уровень чистого пола 1 этажа.

5. Наружные стены многослойные выполнены из блоков толщиной 200мм., с эффективным утеплителем 50 мм. и облицовочным кирпичем 120 мм

6. Отделка фасадов.

Наружные стены - облицовочный кирпич.

Цоколь - облицовка керамогранитными плитками.

Кровля - металлопрофиль

Окна и витражи - металлопластиковые.

## Основные строительные показатели .

Наименование	Площадь, м2				Стрительный объем, м3		
	площадь застройки	общая площадь здания			подземная часть	надземная часть	общий
Жилой дом	158,0	156,8			0	750	750

			Индивидуальный жилой дом	050023-AP		
Архитектор	Ткачев		Жилой дом	Стадия	Лист	Листов
				AC	1	
			Общие данные			




			Индивидуальный жилой дом		050023-AP		
Архитектор	Ткачев		Жилой дом			Стадия	Лист
						AC	2
			3D Визуализация				




			Индивидуальный жилой дом		050023-AP		
Архитектор	Ткачев		Жилой дом		Стадия	Лист	Листов
						AC	3
			3D Визуализация				

# ПЛАН 1-ГО ЭТАЖА

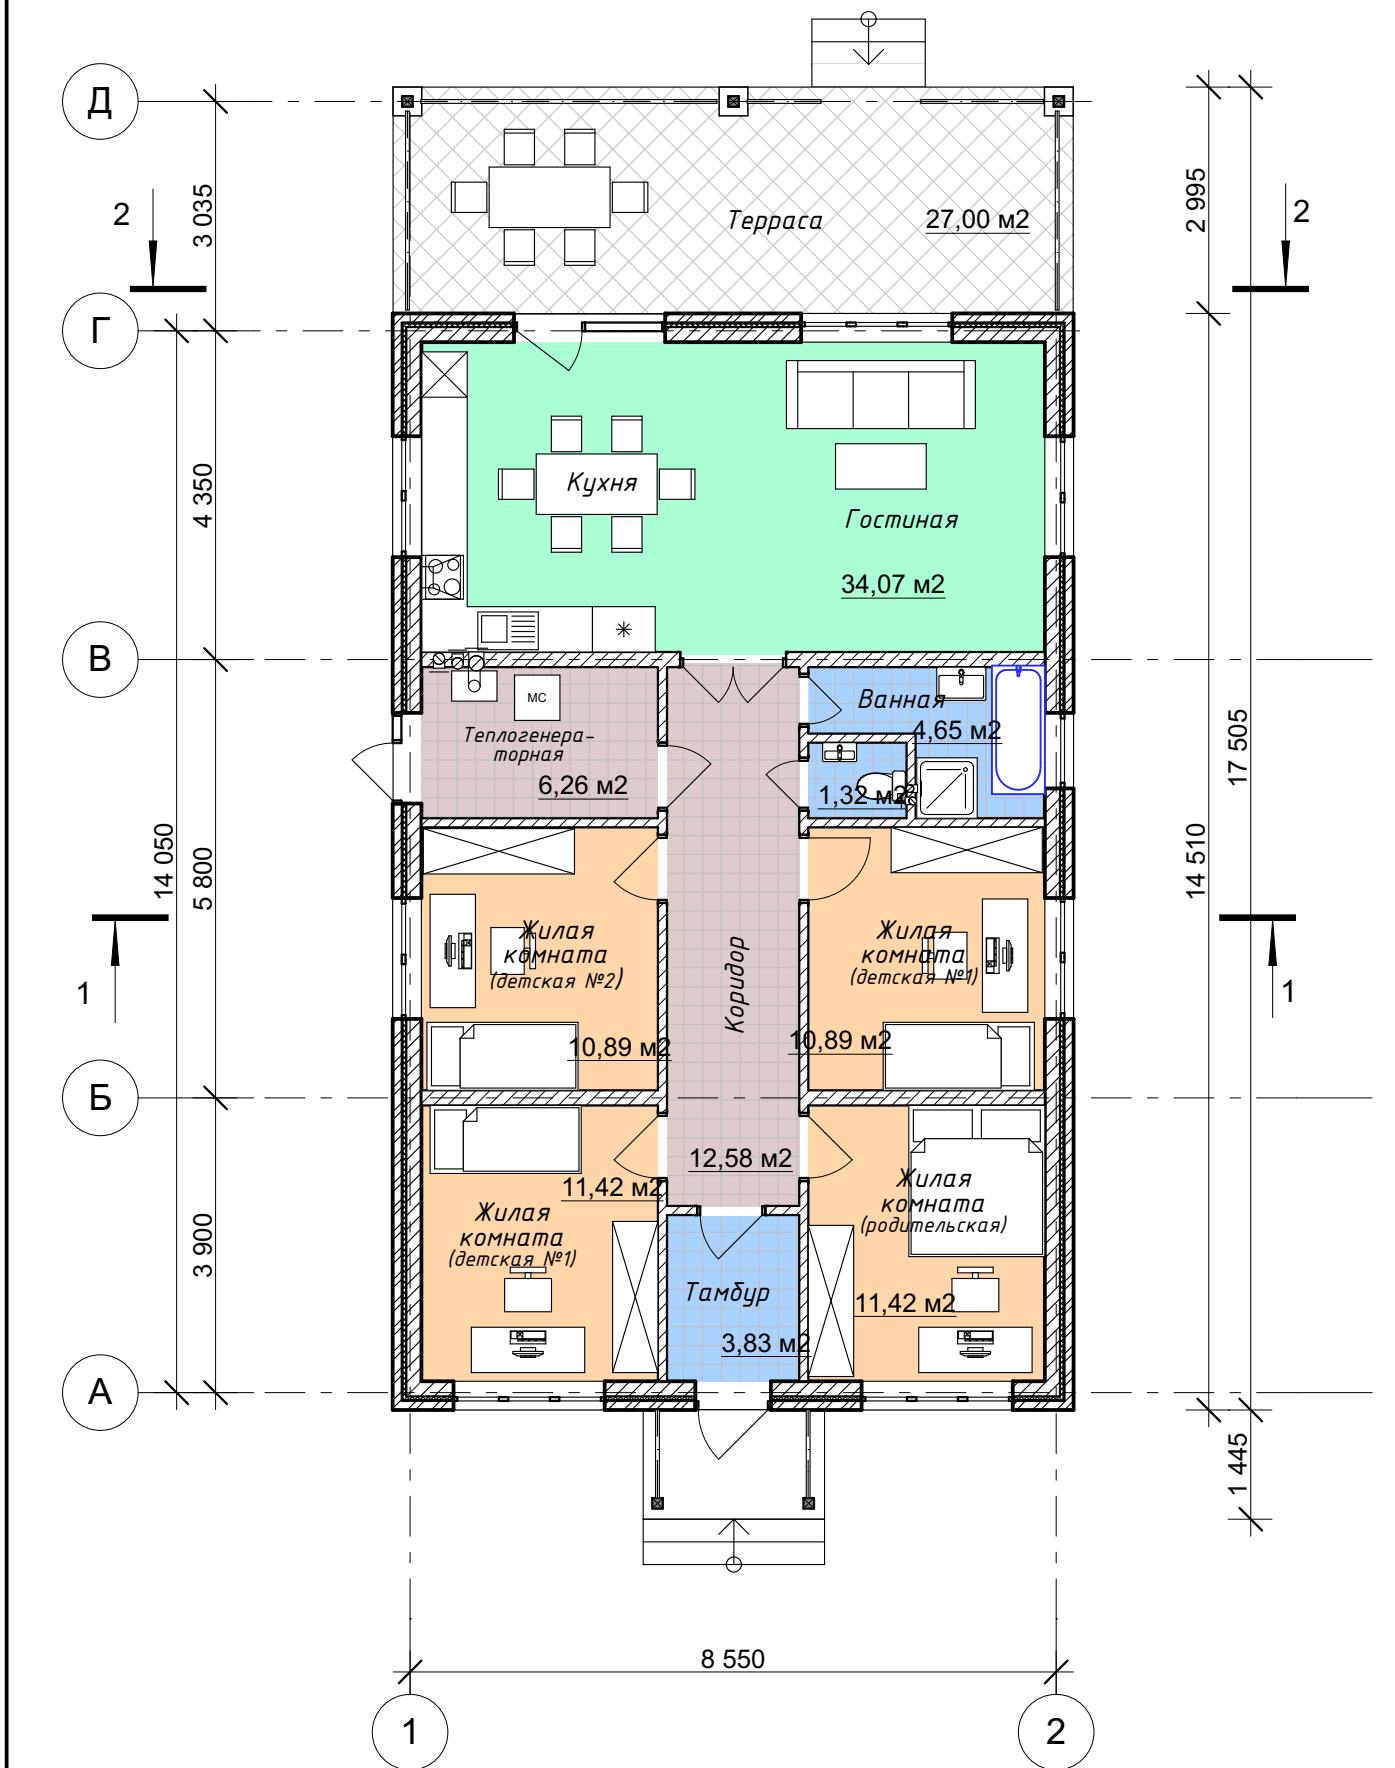


Архитектор	Ткачев	Индивидуальный жилой дом		Стадия	Лист	Листов
Жилой дом		050023-AP		AC		
План 1-го этажа						

## **ПЛАН 1-ГО ЭТАЖА**

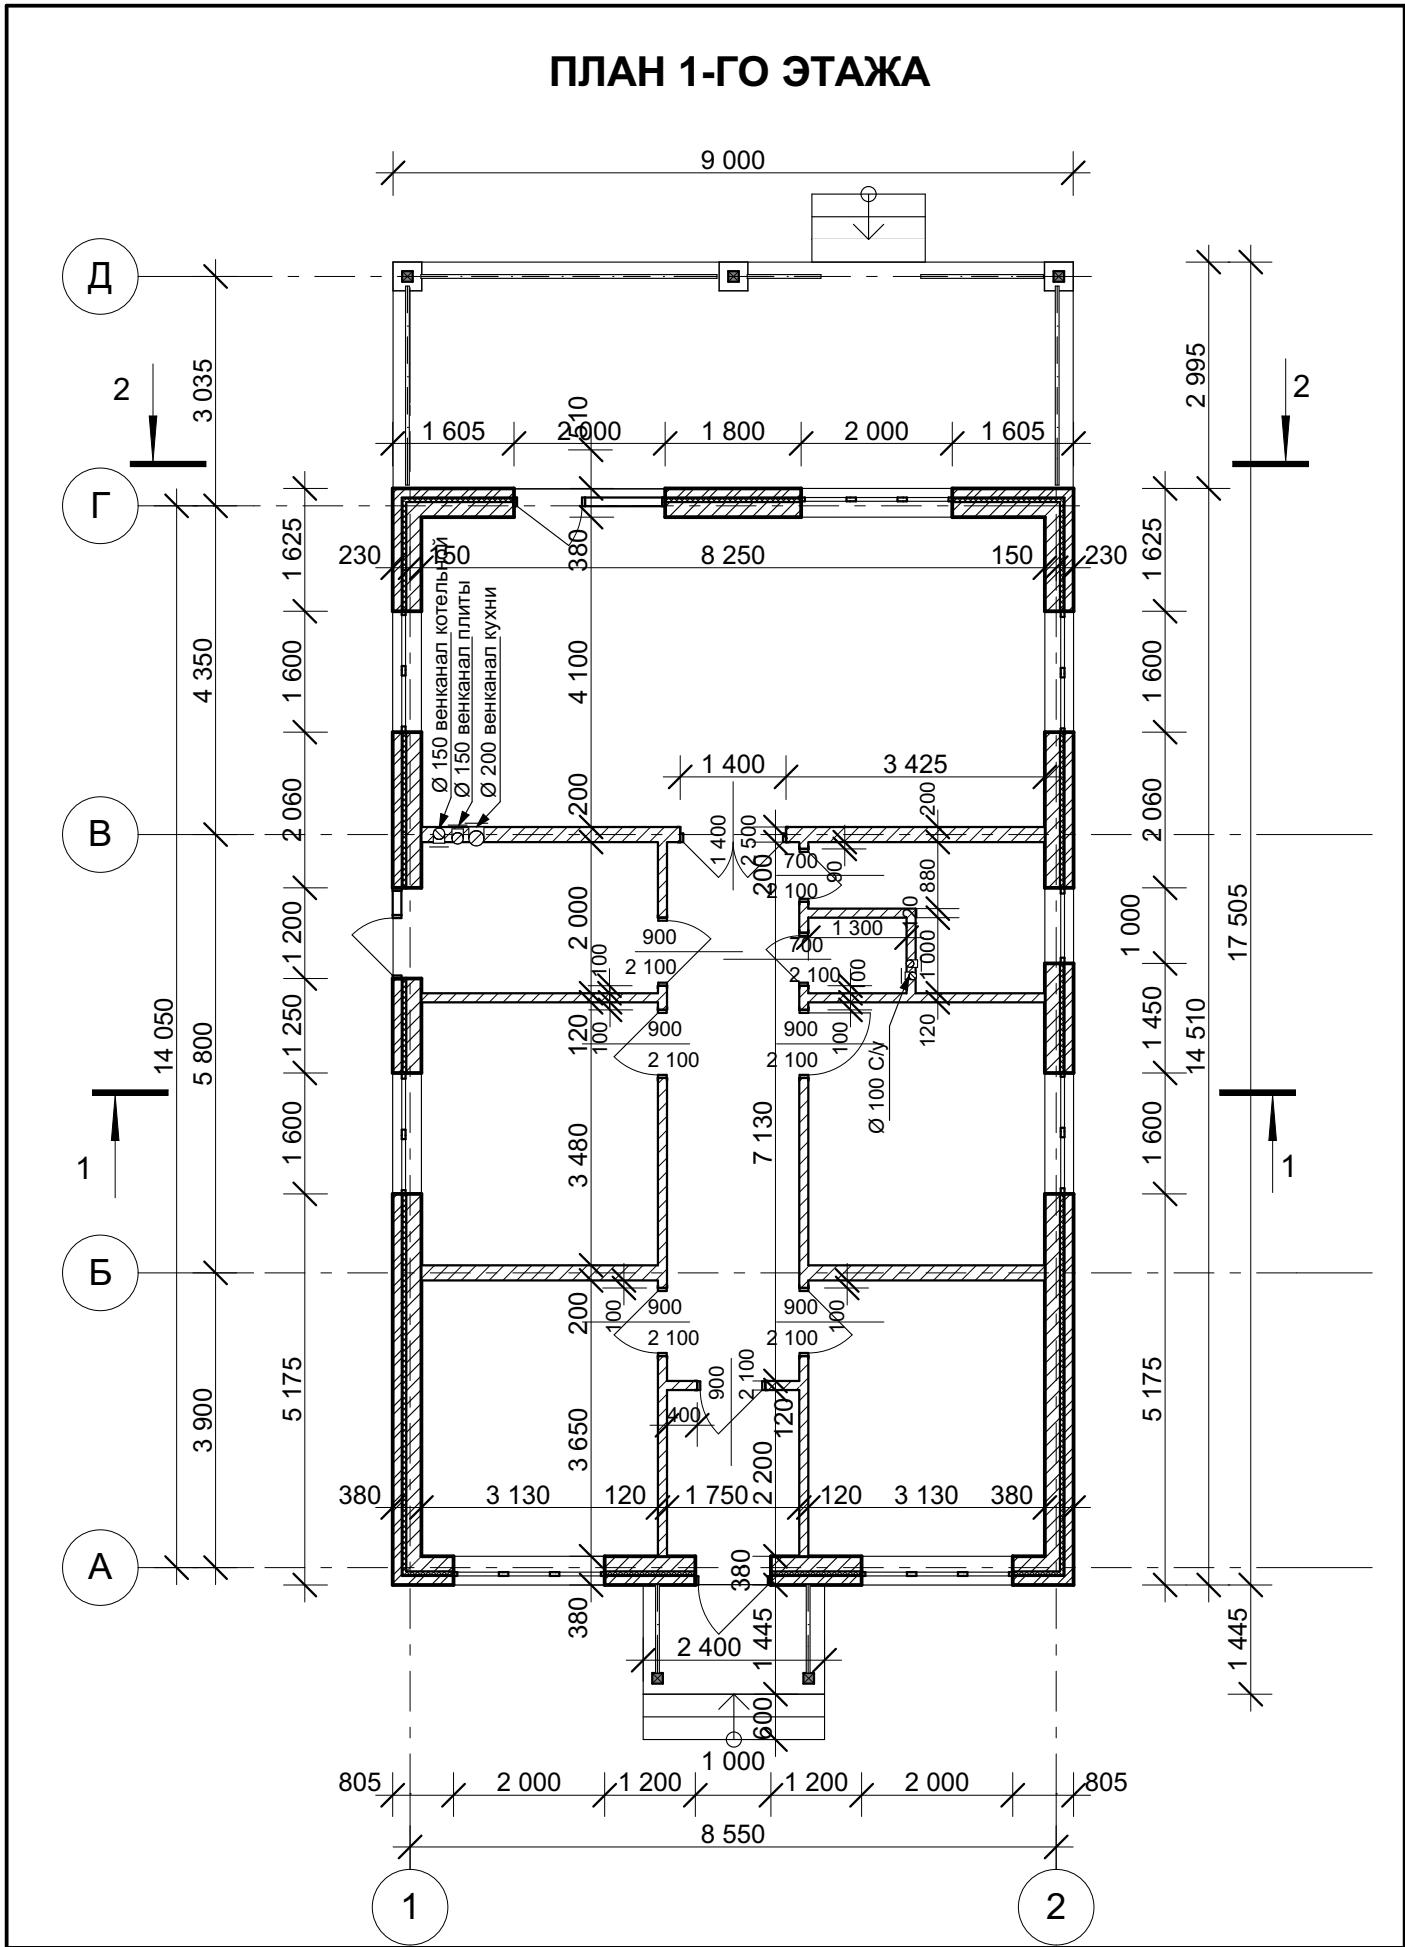


			Индивидуальный жилой дом	050023-AP		
Архитектор	Ткачев		Стадия			Лист
			Жилой дом	AC	5	Листов
			План 1-го этажа - Кладочный			

# ПЛАН КРОВЛИ

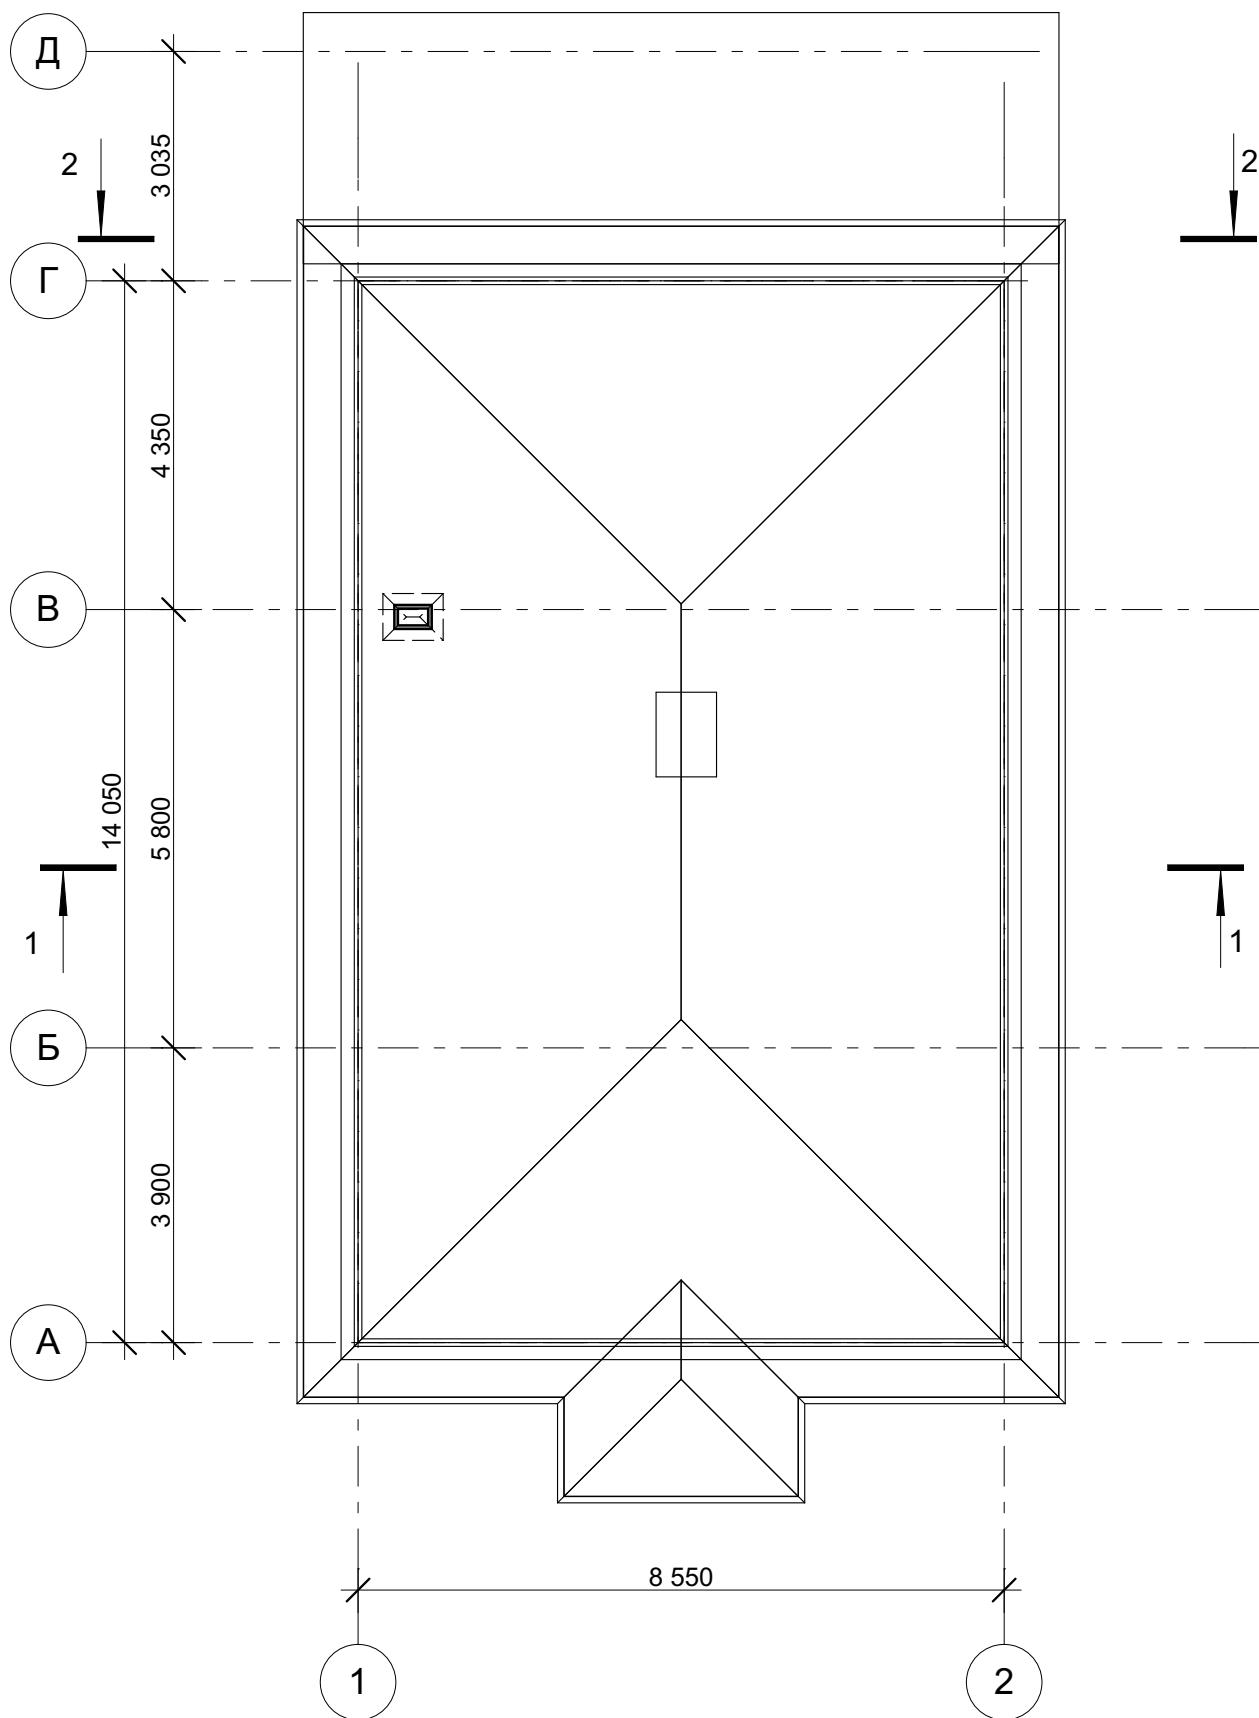


Архитектор	Ткачев	Индивидуальный жилой дом	Стадия	Лист	Листов
		Жилой дом	AC	6	
		План кровли			

## ФАСАД 1-2

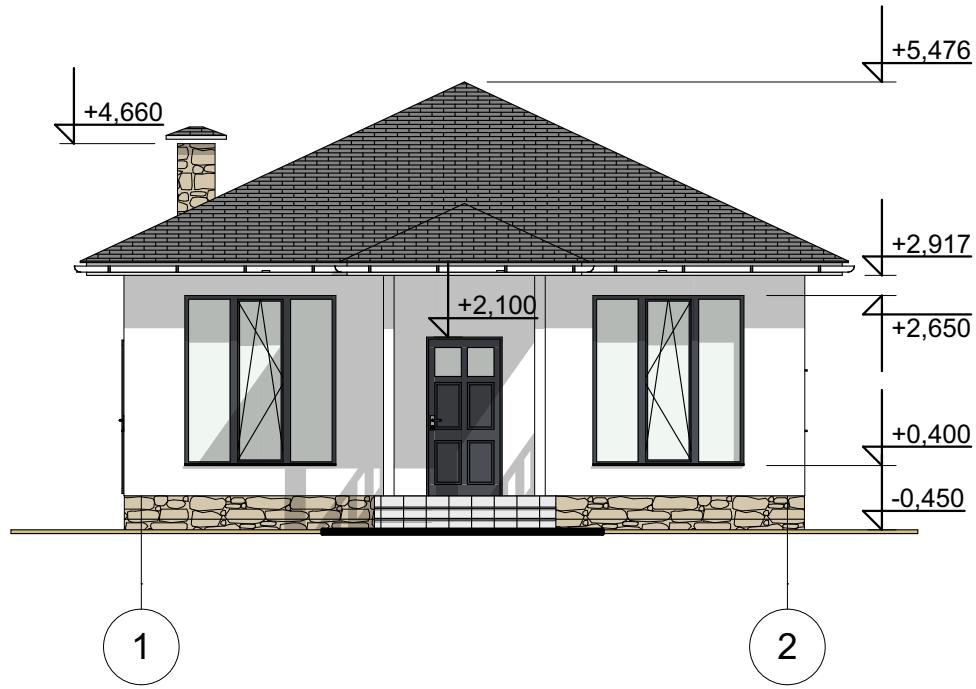

## ФАСАД 2-1

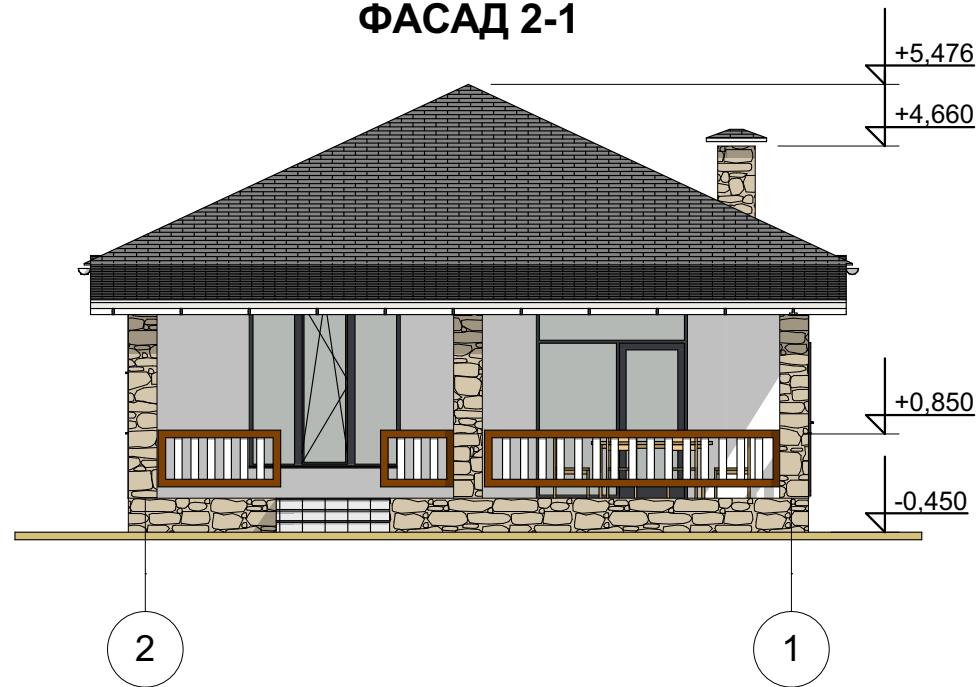

			<i>Индивидуальный жилой дом</i>	050023-AP		
Архитектор	Ткачев		<i>Жилой дом</i>	Стадия	Лист	Листовъ
				AC	7	
			<i>Фасад 1-2, 2-1</i>			

## ФАСАД А-Г




## ФАСАД Г-А




			<i>Индивидуальный жилой дом</i>	050023-AP		
Архитектор	Ткачев		<i>Жилой дом</i>	Стадия	Лист	Листов
				AC	8	

### РАЗРЕЗ 1-1

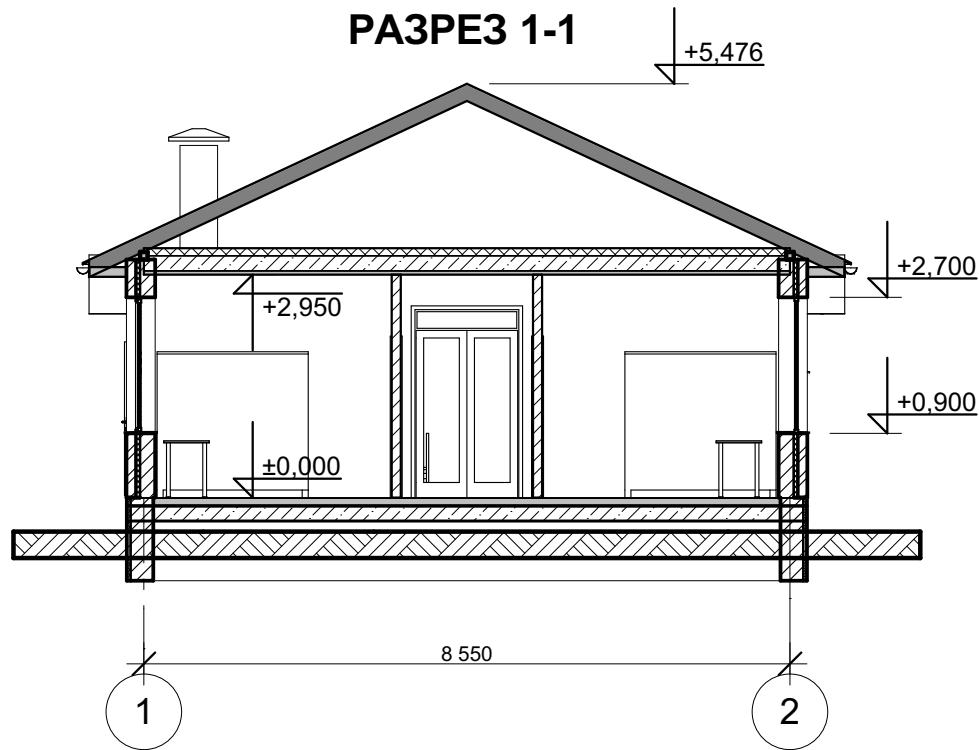

### Разрез 2-2

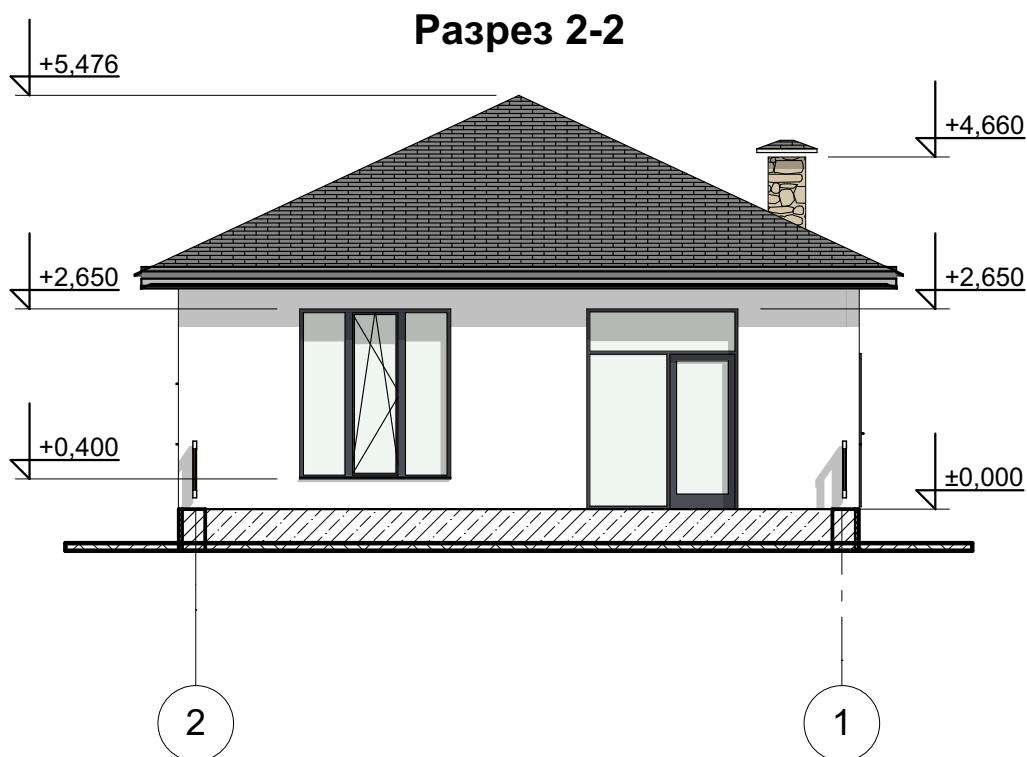

			Индивидуальный жилой дом	050023-AP		
Архитектор	Ткачев			Стадия	Лист	Листов
Жилой дом			AC 9			
Разрез 1-1,						