

ПРОЕКТНАЯ ДОКУМЕНТАЦИЯ

Индивидуальный жилой дом

Эскизный проект
"Архитектурные решения"
010023-AP



Ведомость листов комплекта марки АР.

Лист	Наименование	Примечание
1	Общие данные.	
2	3D Визуализация	
3	3D Визуализация	
4	План первого этажа (мебель).	
5	План первого этажа (кладочный).	
6	План кровли	
7	Разрез 1-1	
8	Фасад 1-4, Фасад 4-1	
9	Фасад А-В, Фасад В-А	

Общие указания.

- Проектная документация по объекту «Индивидуальный жилой дом» разработан в стадии "Эскиз" на основании задания на проектирования, утвержденного заказчиком.
- Проект предназначен для строительства в III Б климатическом районе.
- Степень огнестойкости здания II.
Класс здания по функциональной пожарной опасности Ф1.3.
- За нулевую отметку принят уровень чистого пола 1 этажа.
- Наружные стены многослойные выполнены из блоков толщиной 200мм., с эффективным утеплителем 50 мм. и облицовочным кирпичем 120 мм
- Отделка фасадов.
Наружные стены - облицовочный кирпич.
Цоколь - облицовка керамогранитными плитками.
Кровля - металлическая черепица
Окна и витражи - металлопластиковые.

Основные сведения и условия строительства

- климатический район строительства - III Б,
- нормативный вес снегового покрова - 0,00035МПа
- нормативное давление ветра - 0,001 МПа
- расчетная зимняя температура наружного воздуха -13⁰С
- нормативная глубина промерзания грунтов -0,8
- сейсмичность площадки- 8 баллов

Основные строительные показатели .

Наименование	Площадь, м ²				Стрительный объем, м ³		
	площадь застройки	общая площадь здания	жилая площадь зд-я		подземная часть	надземная часть	общий
Жилой дом	96,3	75,23	35,12		385,2	0	385,2

<i>Архитектор</i>	<i>Ткачев</i>		<i>Индивидуальный жилой дом</i>	<i>010023-AP</i>		
				<i>Стадия</i>	<i>Лист</i>	<i>Листов</i>
				<i>AC</i>	<i>1</i>	
			<i>Общие данные</i>			<i>г-к. Анапа 2023 г.</i>




			Индивидуальный жилой дом		010023-AP		
Архитектор	Ткачев				Стадия	Лист	Листов
					AC	2	
3D Визуализация						г-к. Анапа 2023 г.	




			Индивидуальный жилой дом		010023-AP		
Архитектор	Ткачев				Стадия	Лист	Листов
					AC	3	
3D Визуализация						г-к. Анапа 2023 г.	

ПЛАН 1-ГО ЭТАЖА

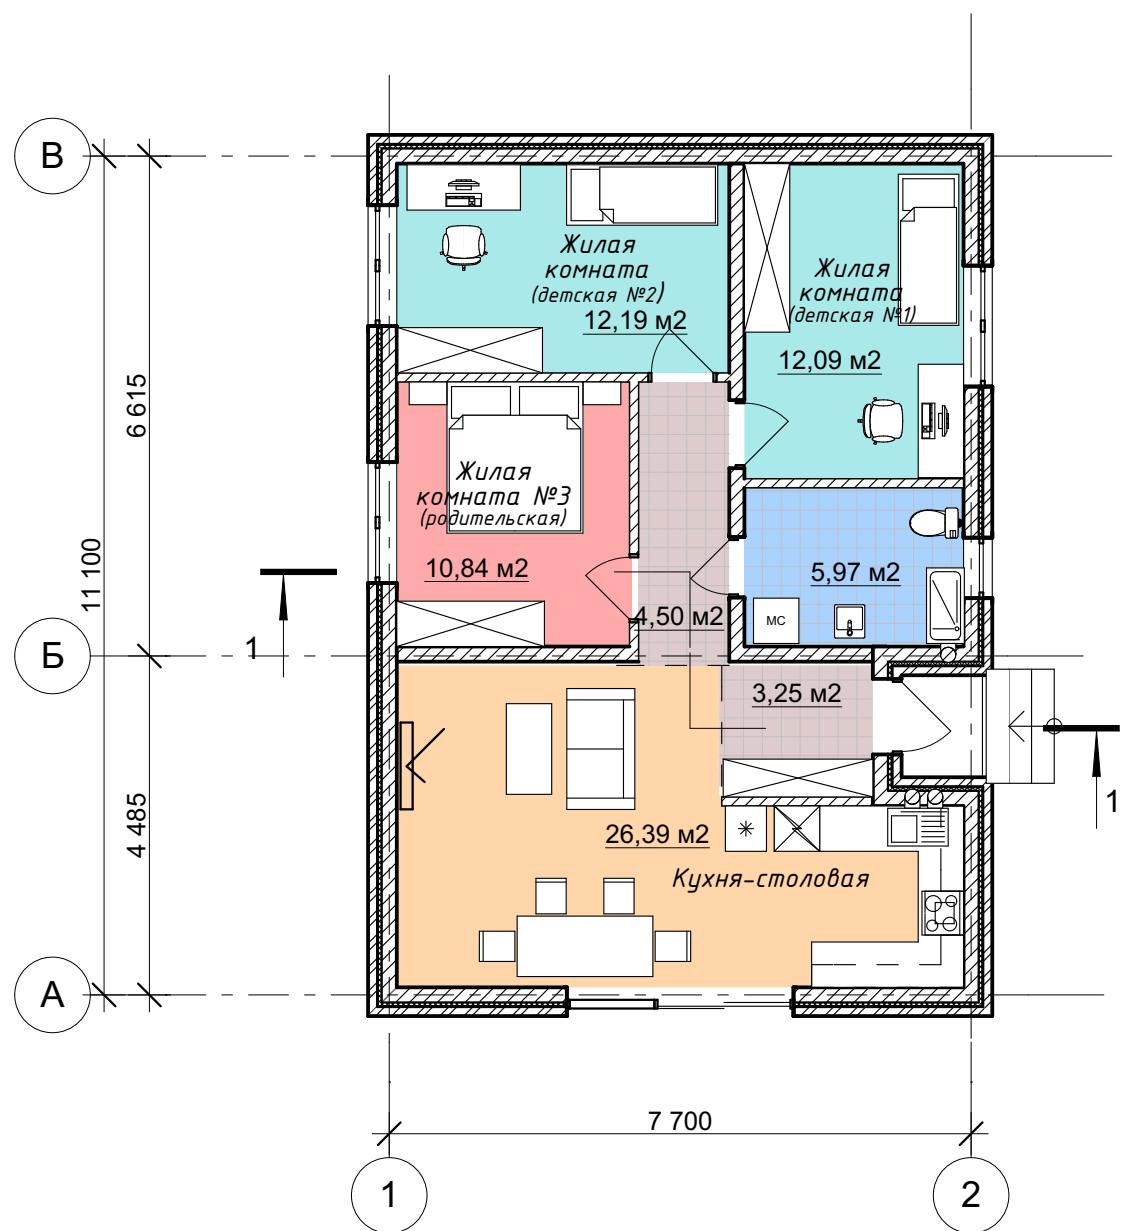


			Индивидуальный жилой дом	010023-AP
Архитектор	Ткачев			
			Стадия	Лист
				Листов
				AC 4
План 1-го этажа (мебель)				г-к. Анапа 2023 г.

ПЛАН 1-ГО ЭТАЖА

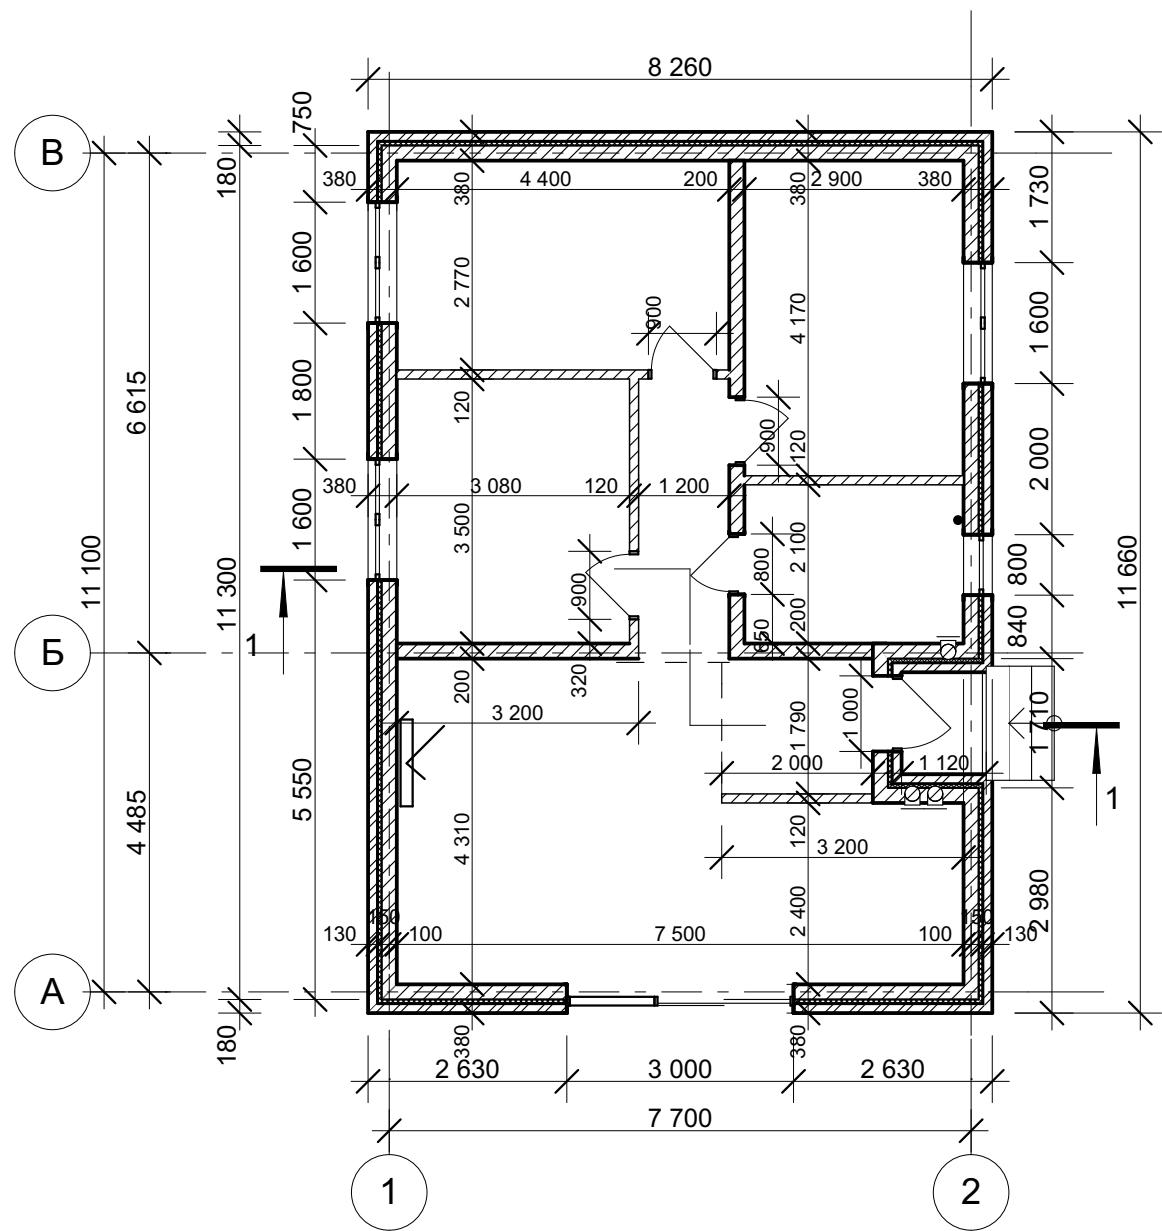


			Индивидуальный жилой дом	010023-AP		
Архитектор	Ткачев					Стадия
						AC
			План 1-го этажа (кладочный)	г-к. Анапа 2023 г.		

ПЛАН КРОВЛИ

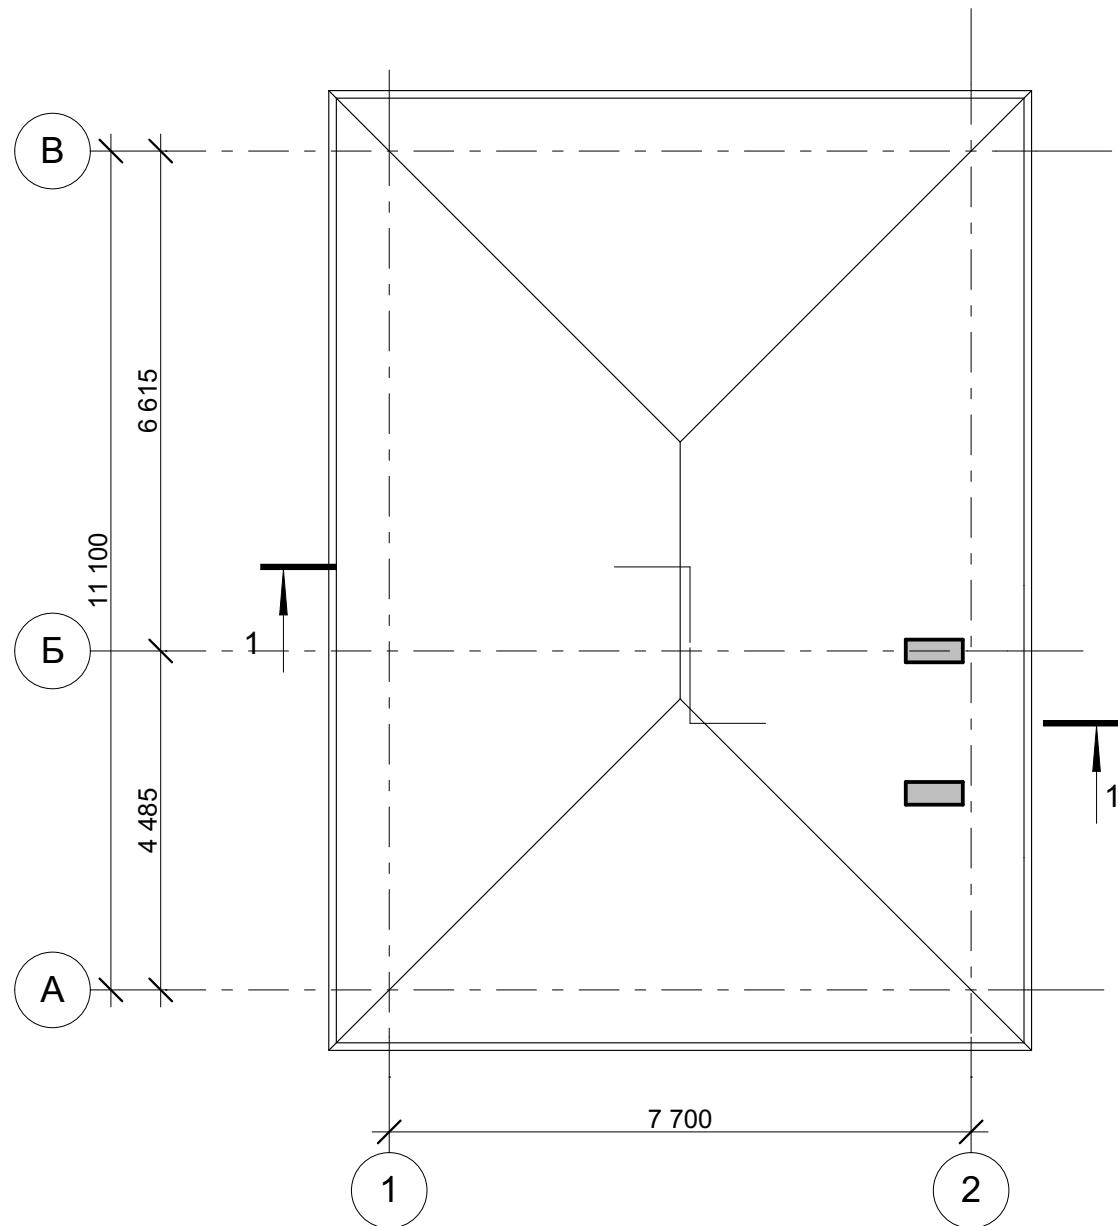


			Индивидуальный жилой дом	010023-AP		
Архитектор	Ткачев					Стадия
						Лист
						Листов
						AC 6
			План кровли			г-к. Анапа 2023 г.

РАЗРЕЗ 1-1

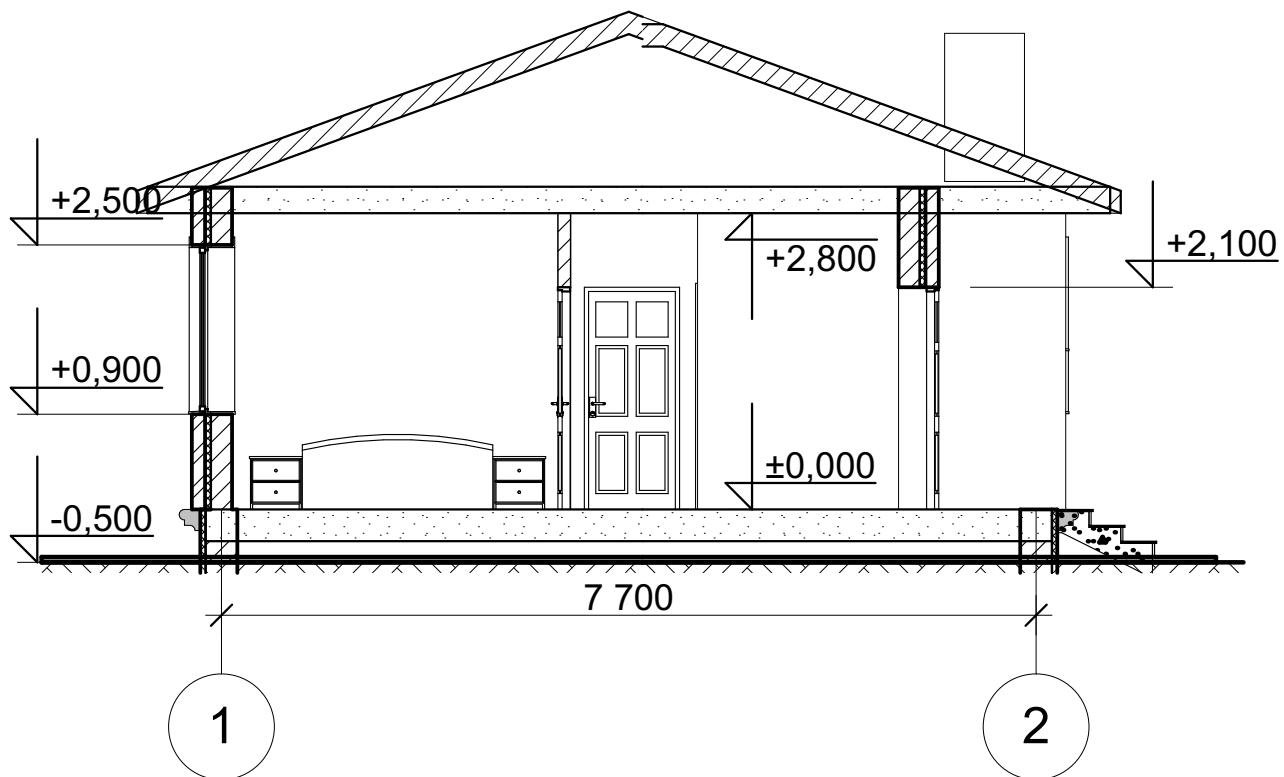


			Индивидуальный жилой дом		010023-AP		
Архитектор	Ткачев					Стадия	Лист
						AC	7
			Разрез 1-1			г-к. Анапа 2023 г.	

ФАСАД 1-2

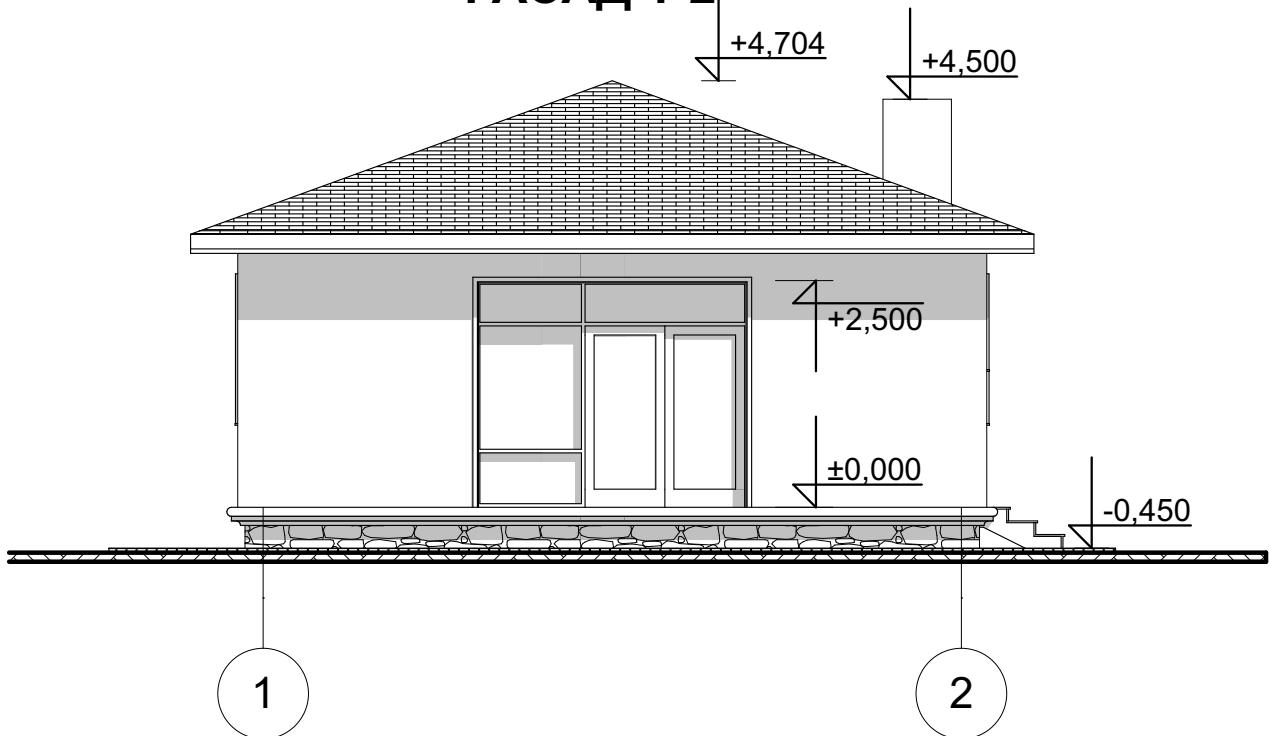


ФАСАД 2-1

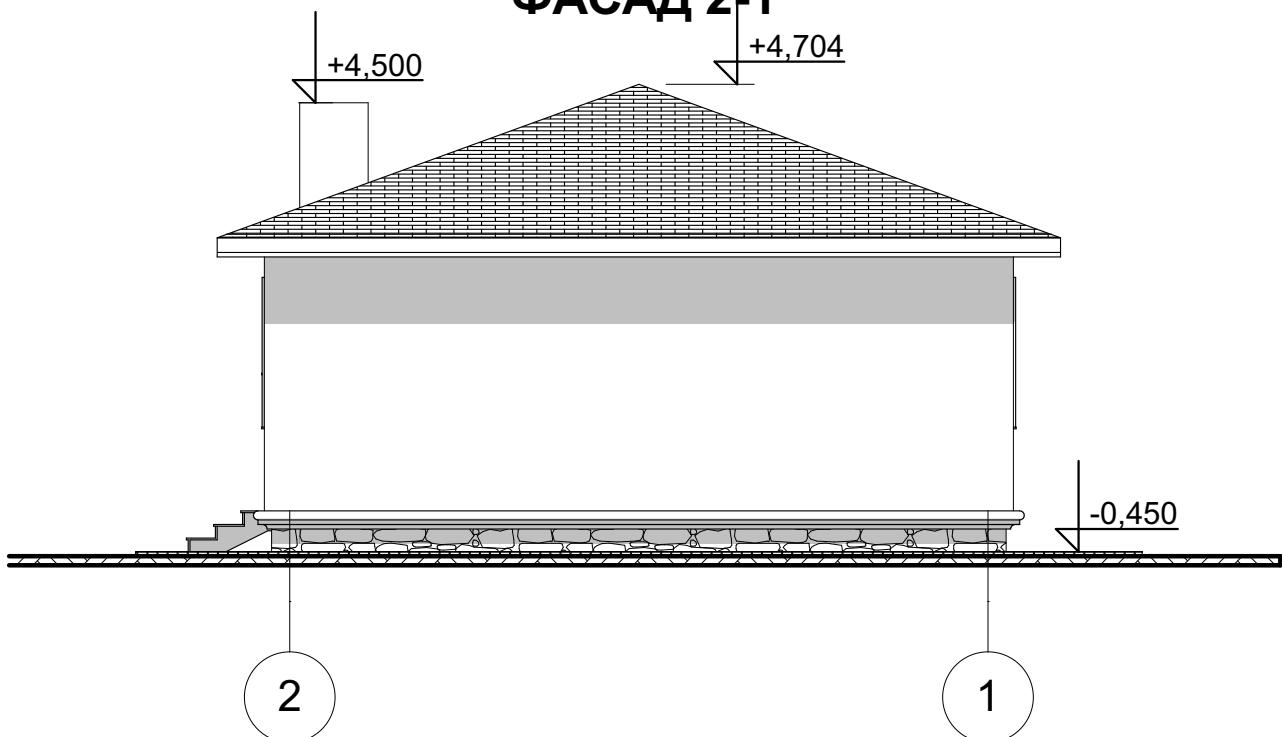


			Индивидуальный жилой дом	010023-AP		
Архитектор	Ткачев			Стадия	Лист	Листов
				АС	8	
Фасад 1-2, 2-1			г-к. Анапа 2023 г.			

ФАСАД А-В

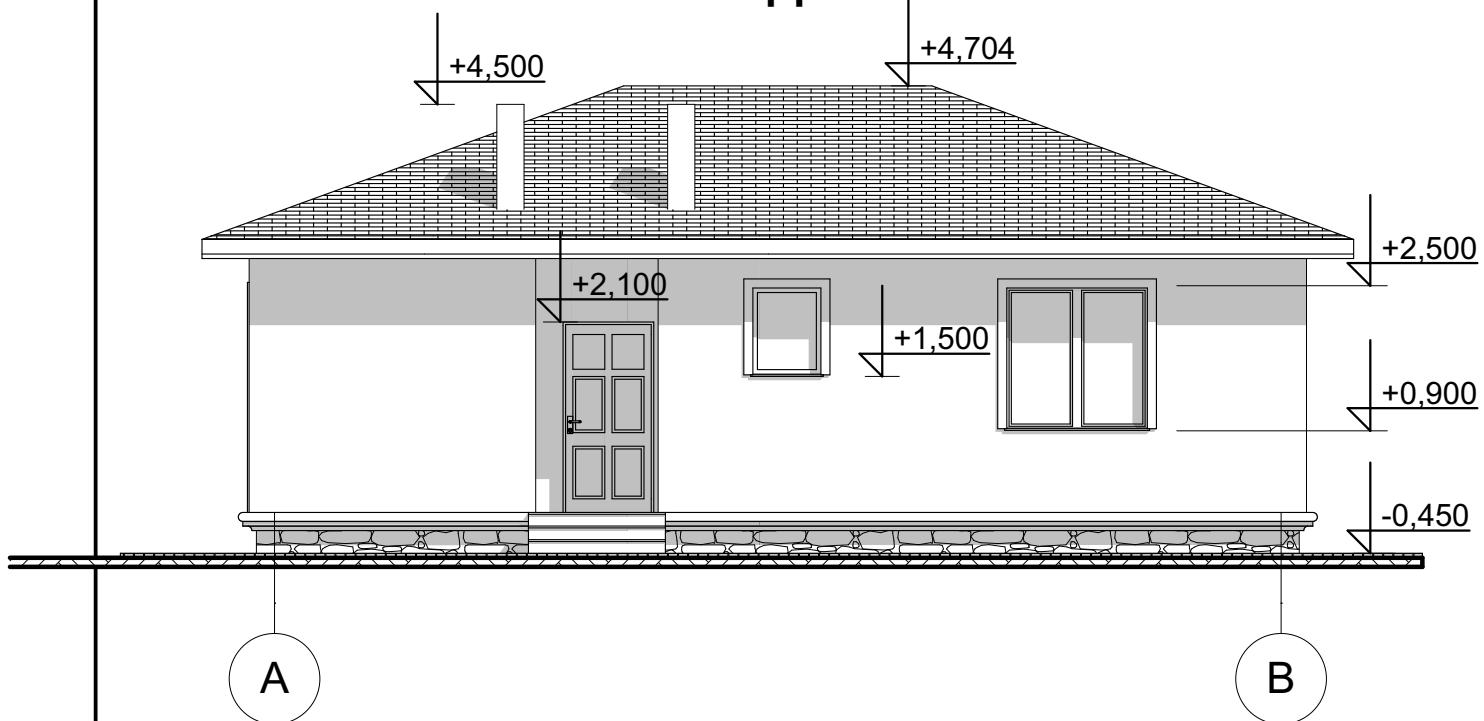

ФАСАД В-А

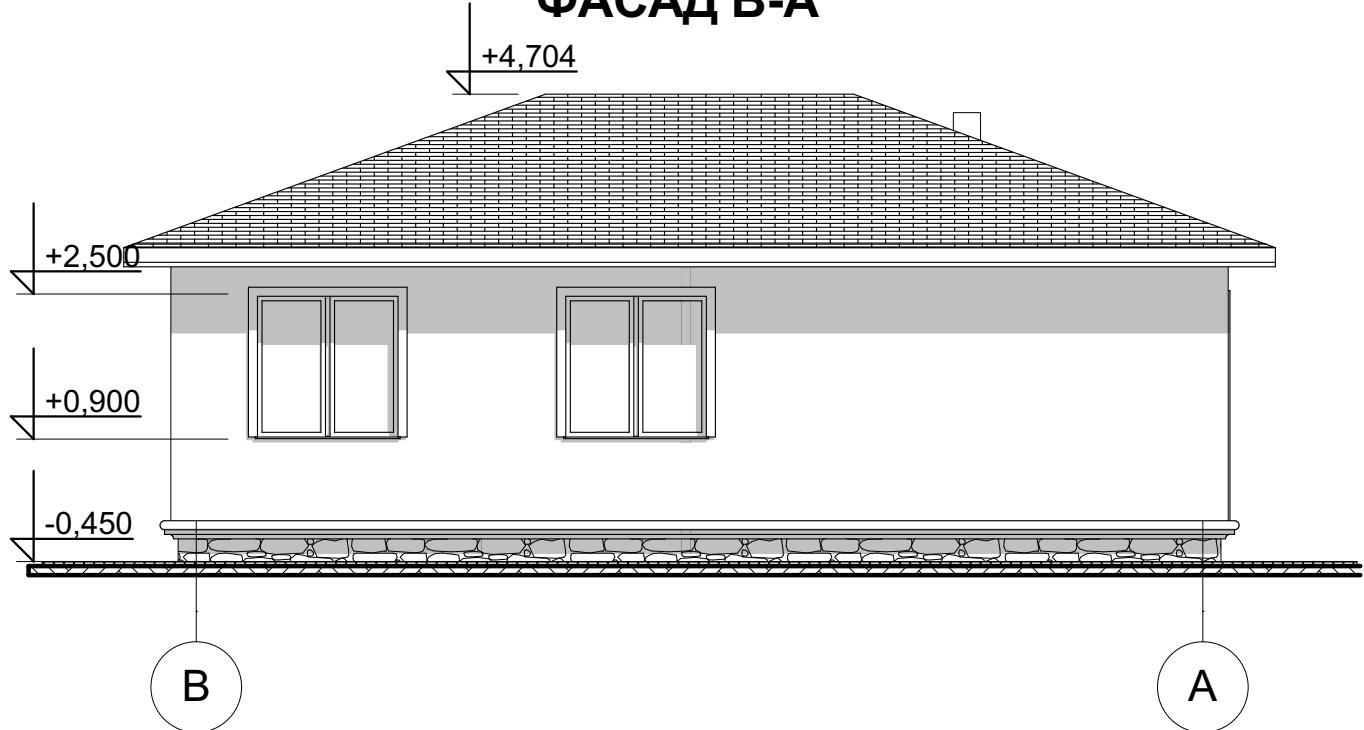

			Индивидуальный жилой дом		010023-AP	
Архитектор	Ткачев				Стадия	Лист
					AC	9
			Фасад А-Б, Б-А		г-к. Анапа 2023 г.	